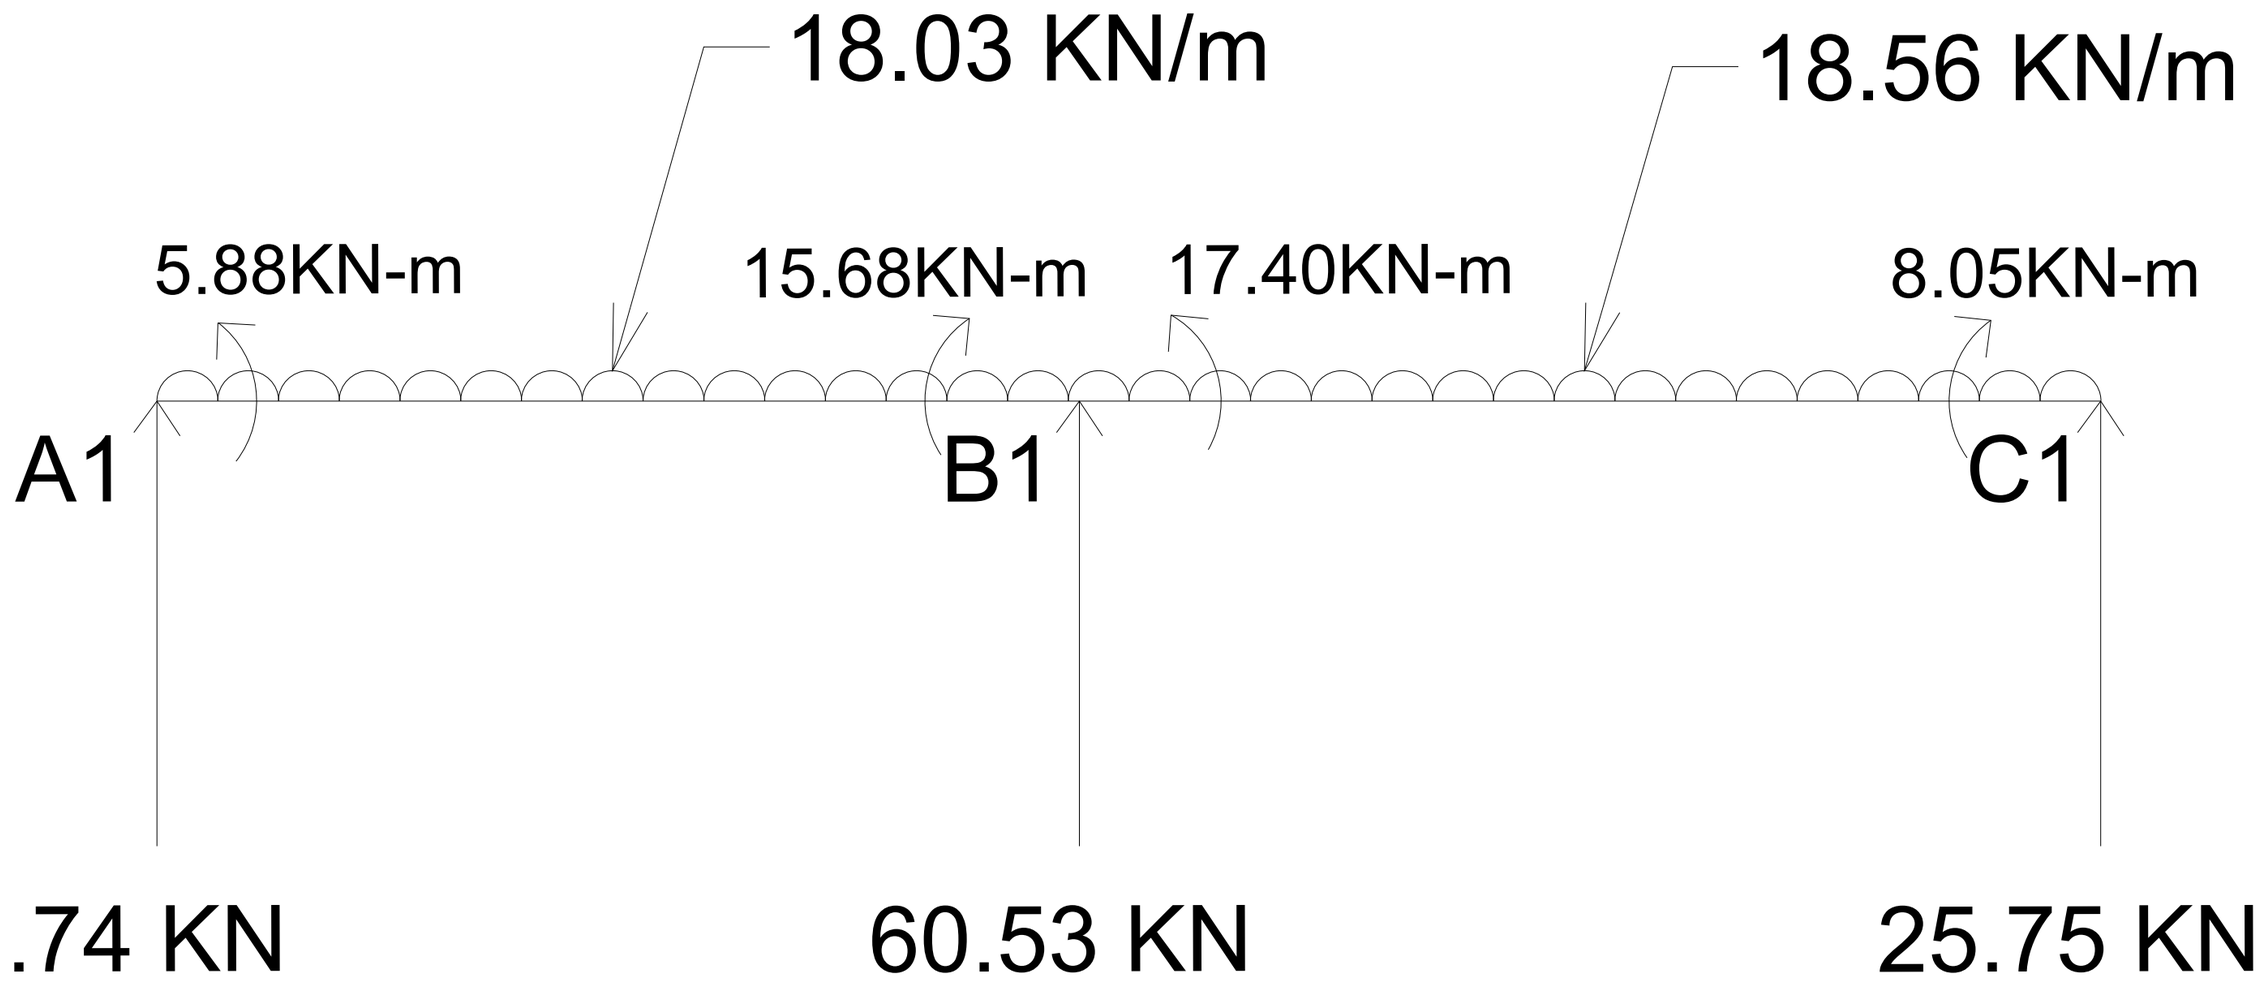

18.03 KN/m
18.56 KN/m
5.88KN-m
15.68KN-m
17.40KN-m
8.05KN-m
A1
B1
C1
21.74 KN
60.53 KN
25.75 KN