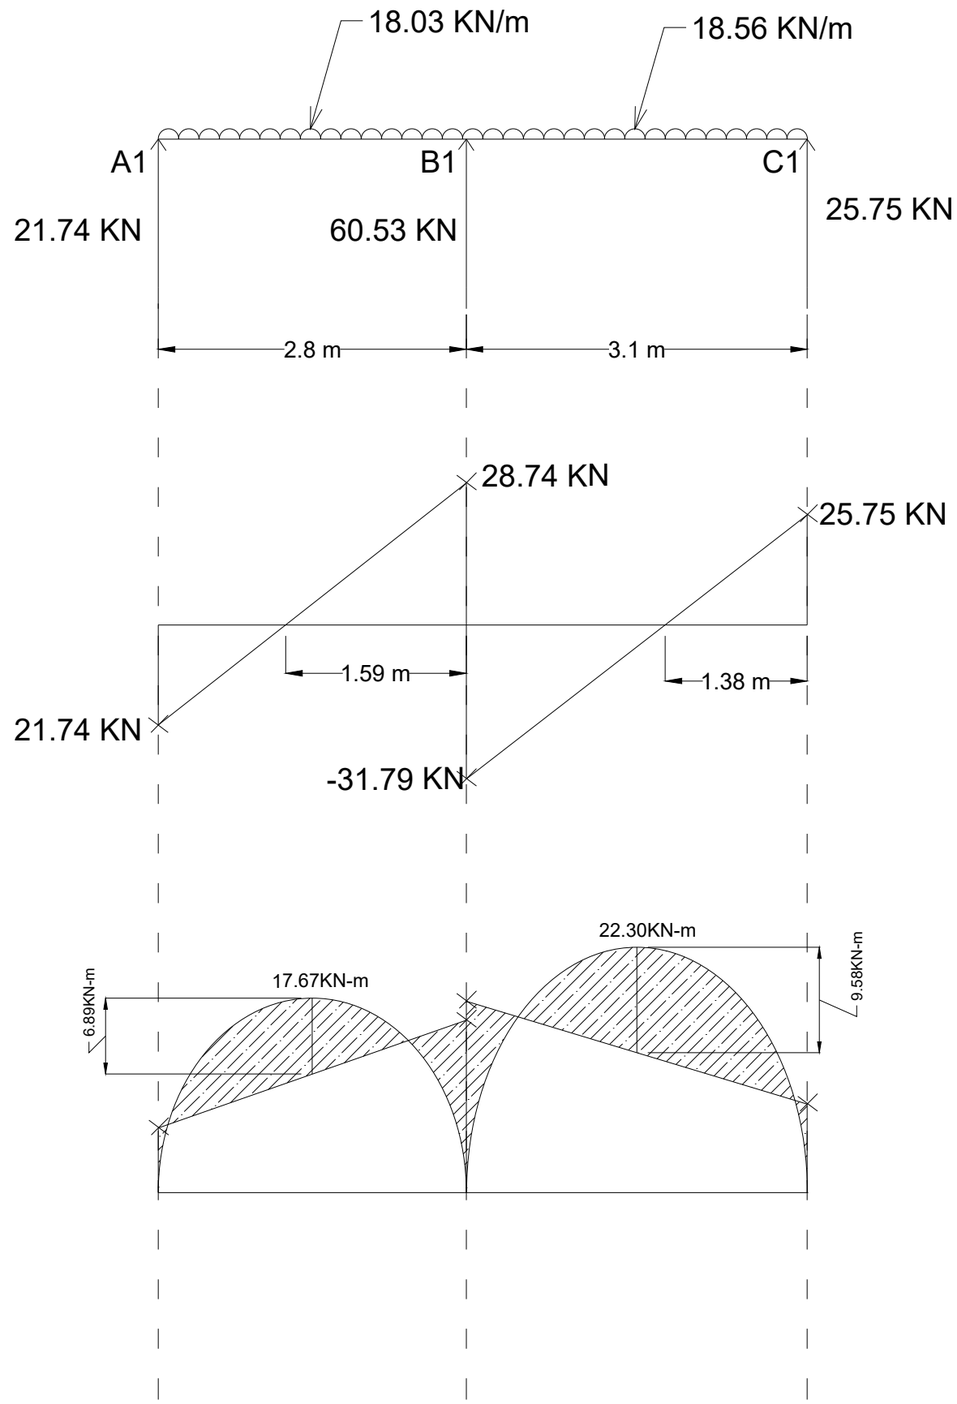

18.03 KN/m
18.56 KN/m
A1
B1
C1
21.74 KN
60.53 KN
25.75 KN
2.8 m
3.1 m
28.74 KN
25.75 KN
1.59 m
1.38 m
21.74 KN
-31.79 KN
22.30KN-m
17.67KN-m
6.89KN-m
9.58KN-m