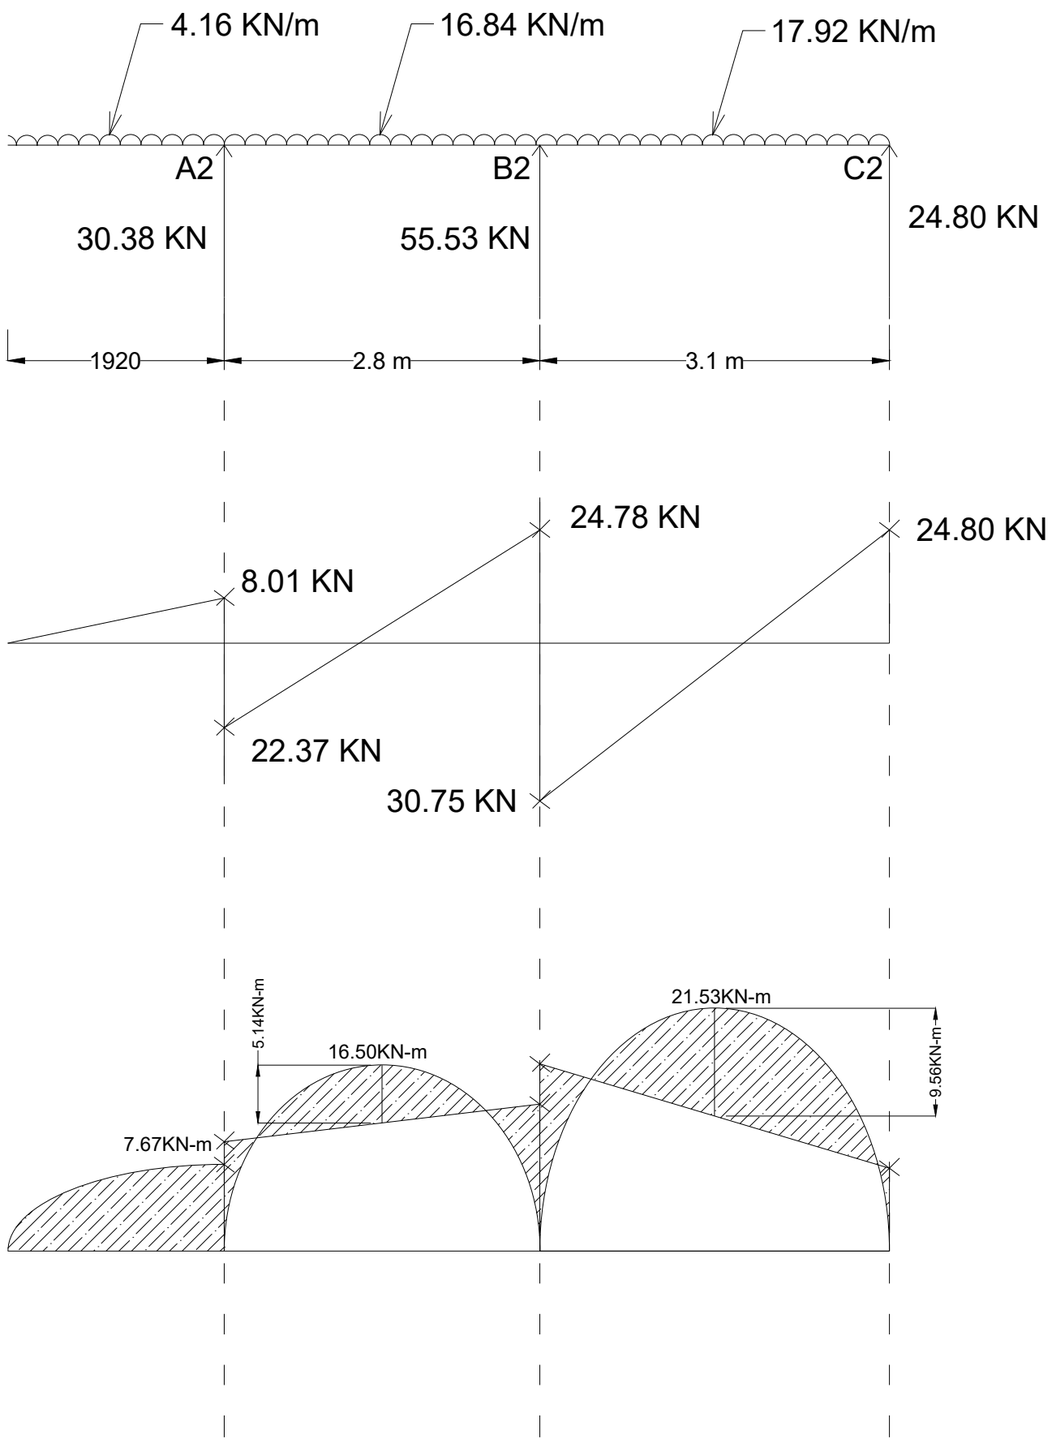

4.16 KN/m
16.84 KN/m
17.92 KN/m
A2
B2
C2
30.38 KN
55.53 KN
24.80 KN
1920
2.8 m
3.1 m
24.78 KN
24.80 KN
8.01 KN
22.37 KN
30.75 KN
5.14KN-m
16.50KN-m
21.53KN-m
9.56KN-m
7.67KN-m