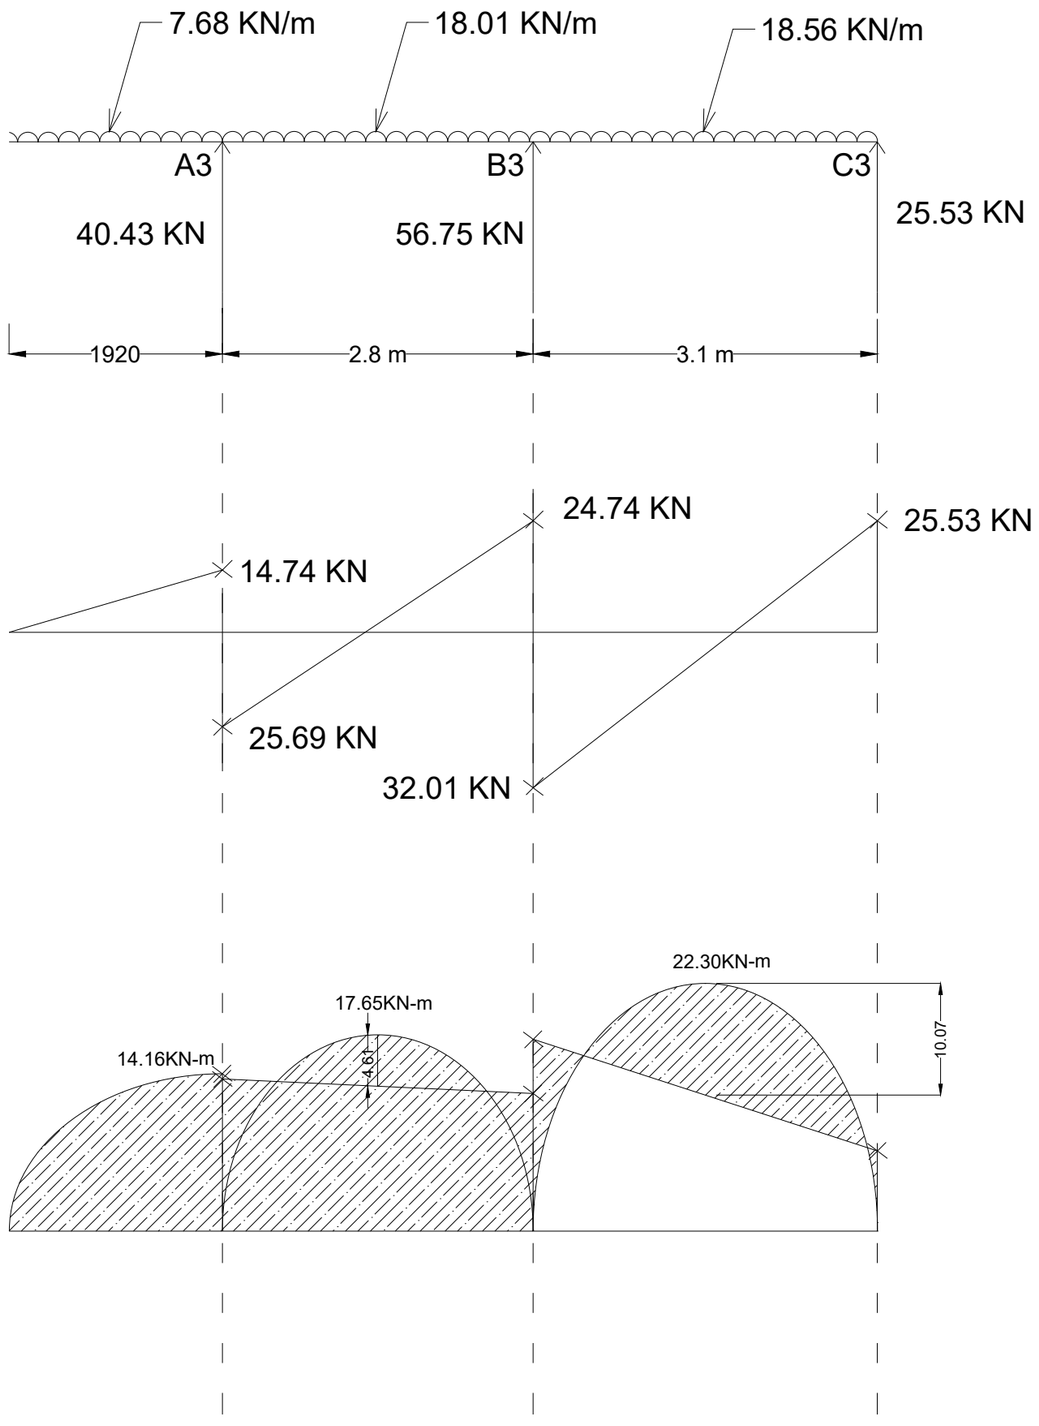

7.68 KN/m
18.01 KN/m
18.56 KN/m
A3
B3
C3
40.43 KN
56.75 KN
25.53 KN
1920
2.8 m
3.1 m
14.74 KN
24.74 KN
25.53 KN
25.69 KN
32.01 KN
14.16KN-m
17.65KN-m
4.61
22.30KN-m
10.07