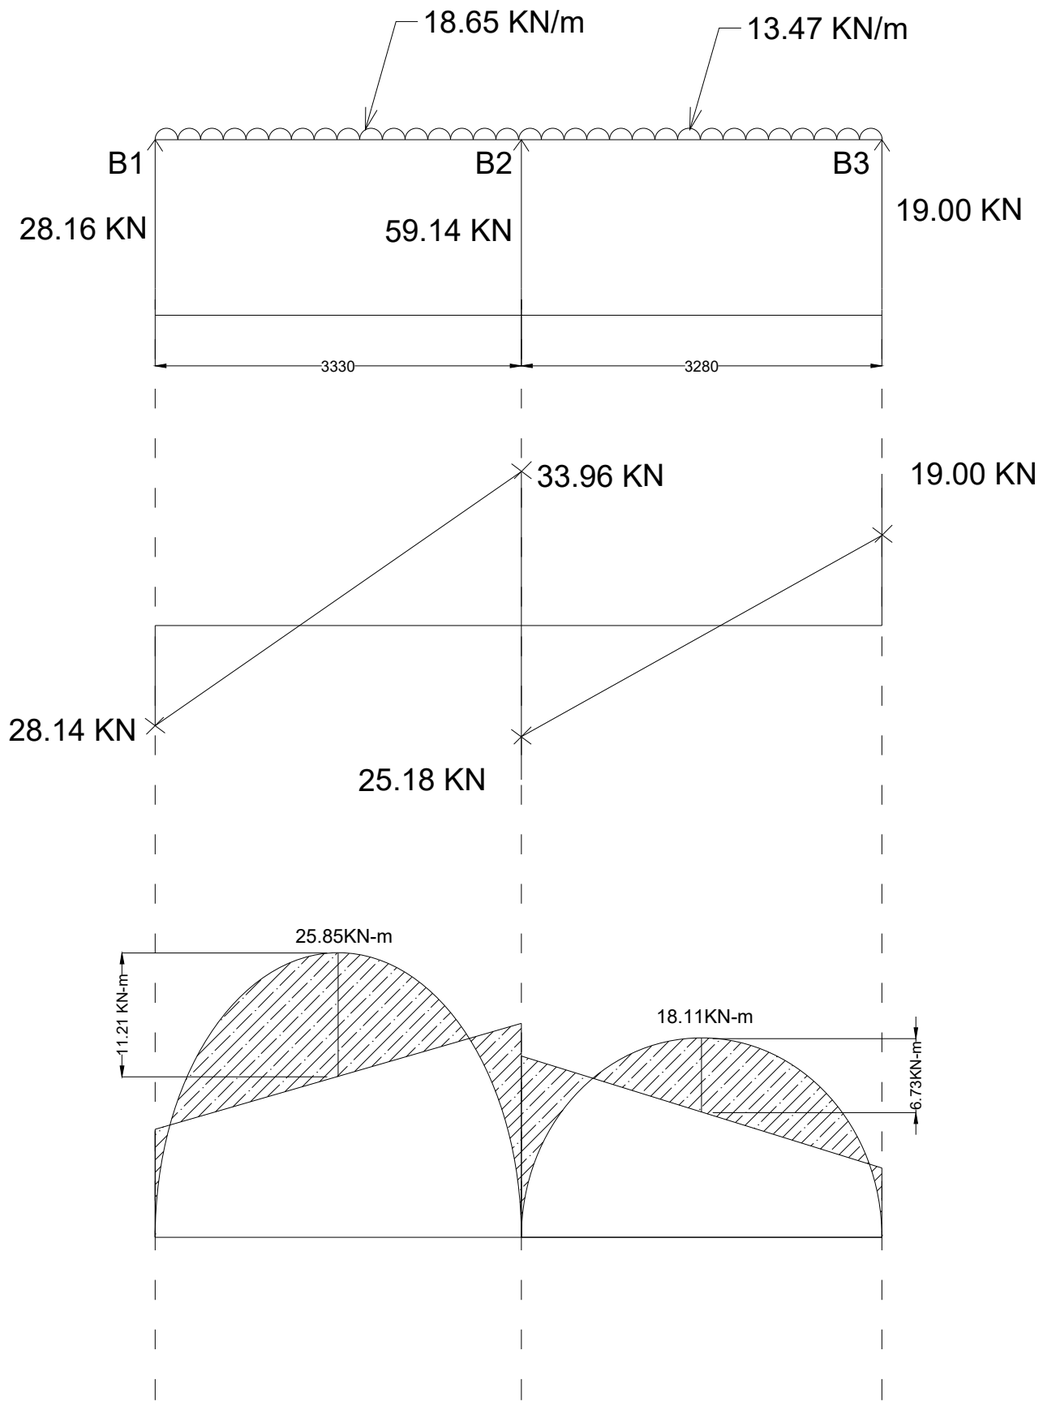

18.65 KN/m
13.47 KN/m
B1
B2
B3
28.16 KN
59.14 KN
19.00 KN
3330
3280
33.96 KN
19.00 KN
28.14 KN
25.18 KN
25.85KN-m
11.21 KN-m
18.11KN-m
6.73KN-m