

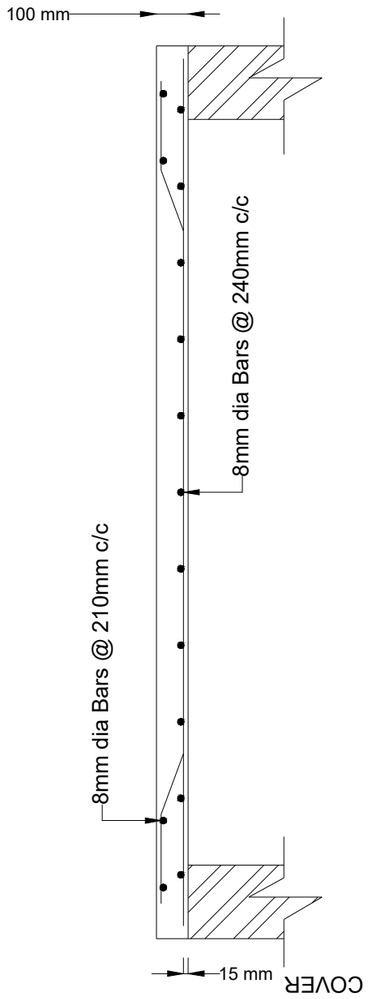


Section - AA

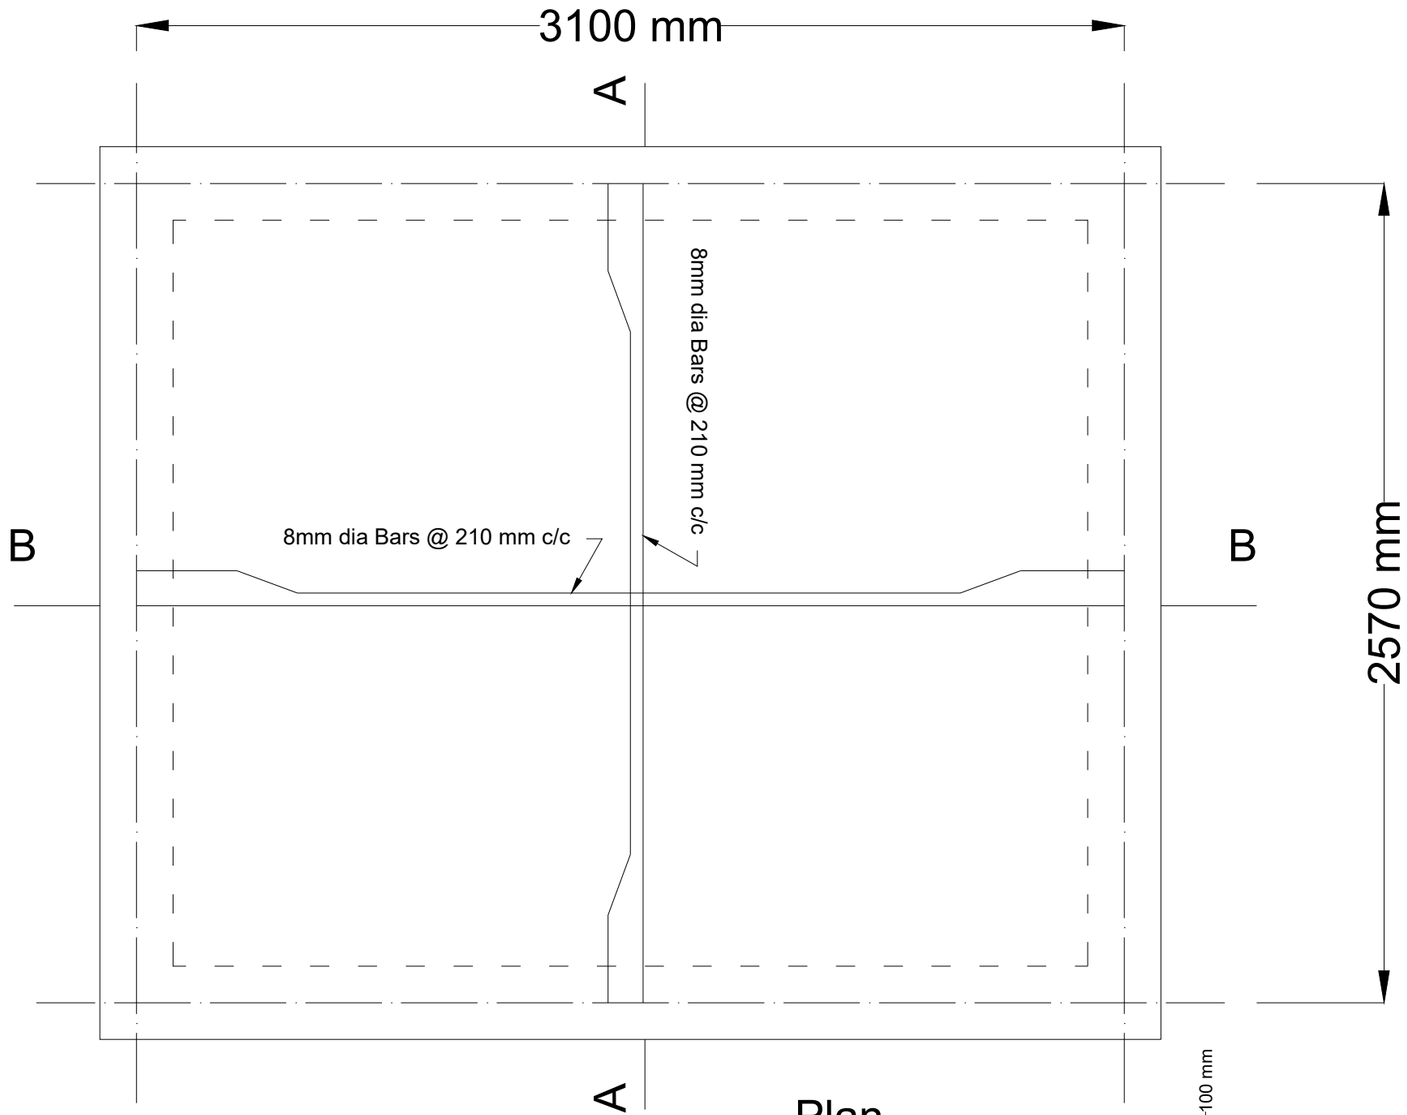

Plan

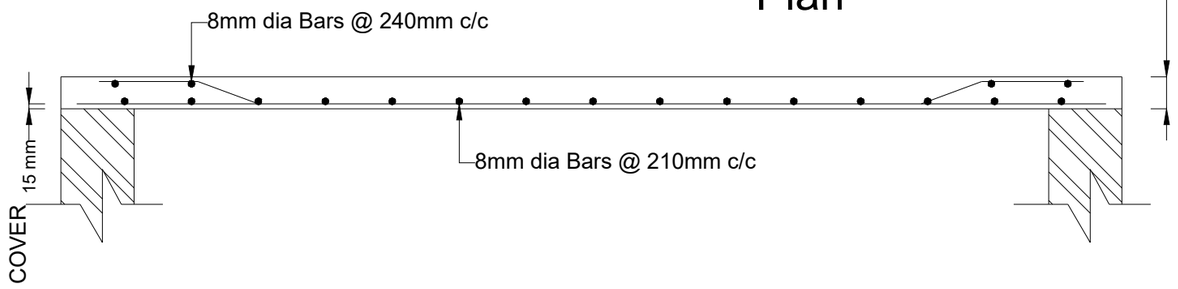

Section - BB