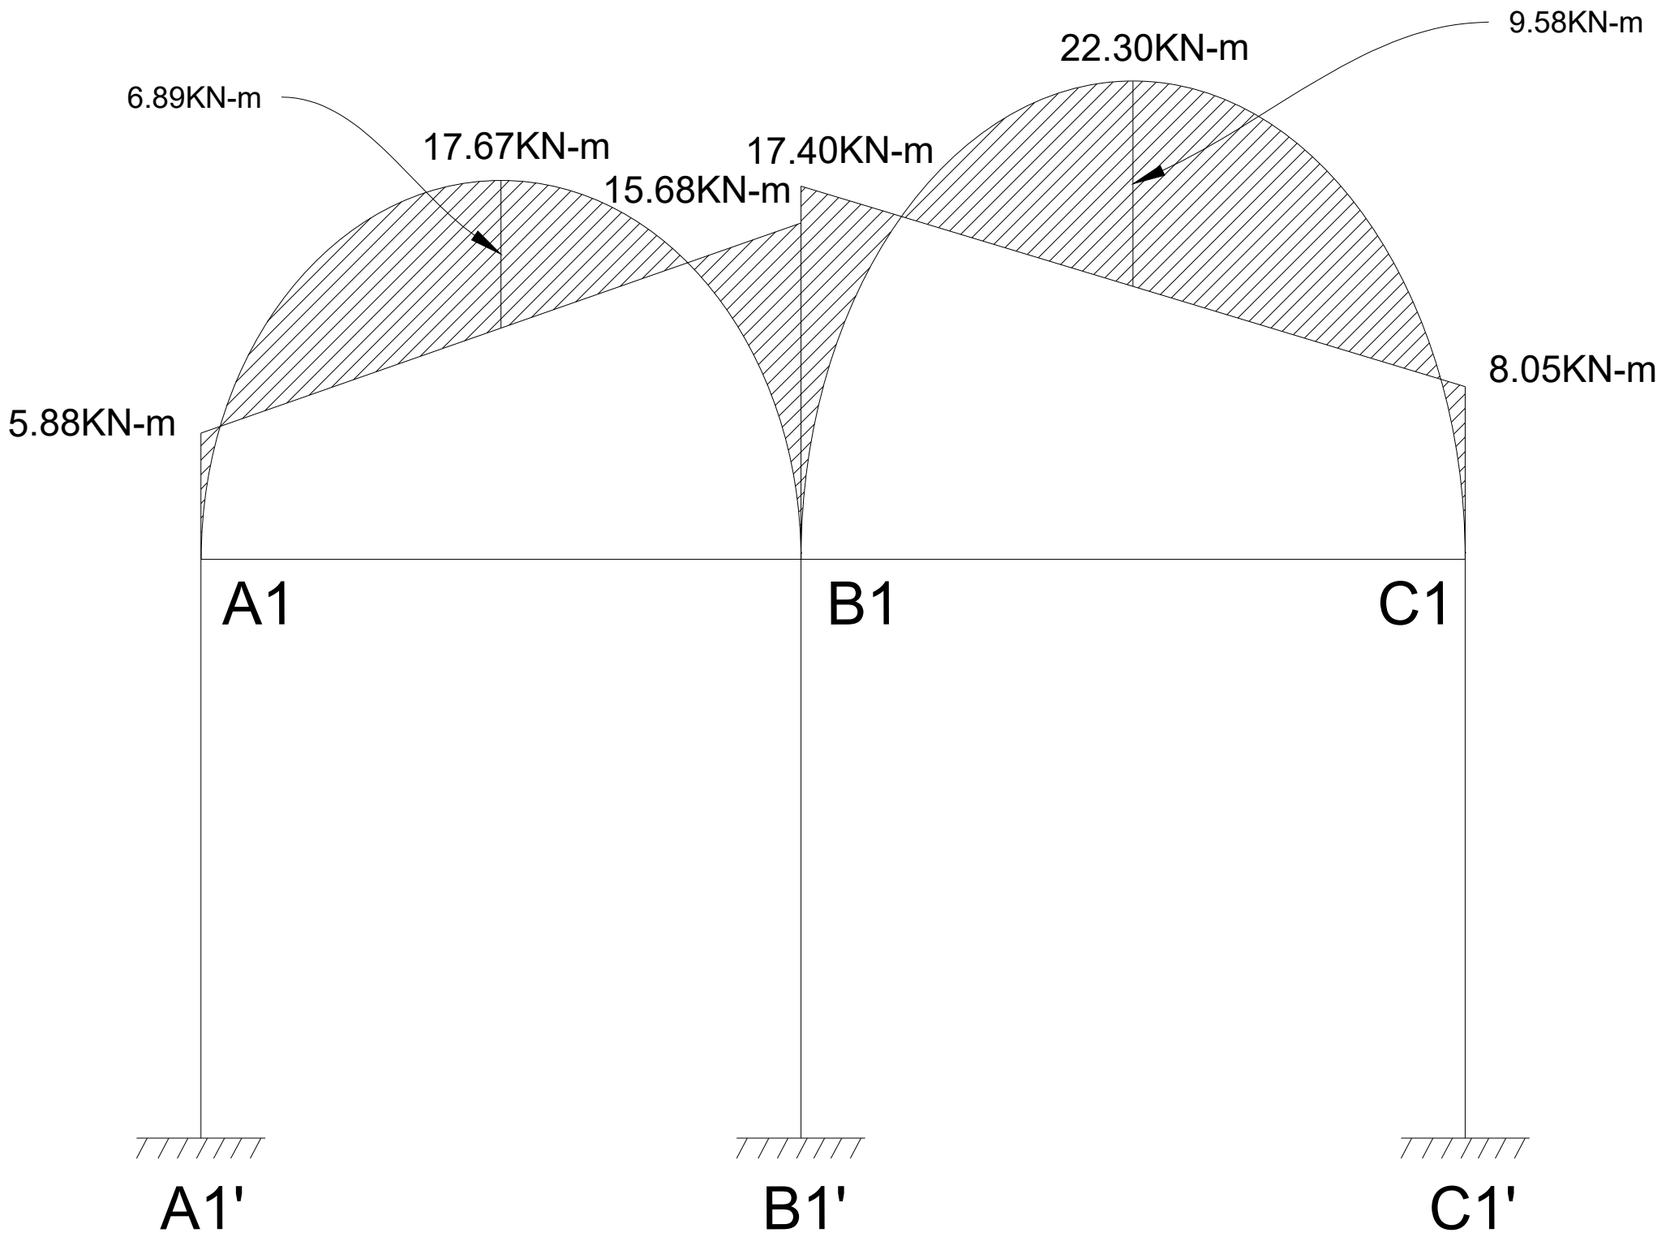

9.58KN-m
22.30KN-m
6.89KN-m
17.67KN-m
17.40KN-m
15.68KN-m
8.05KN-m
5.88KN-m
A1
B1
C1
A1'
B1'
C1'