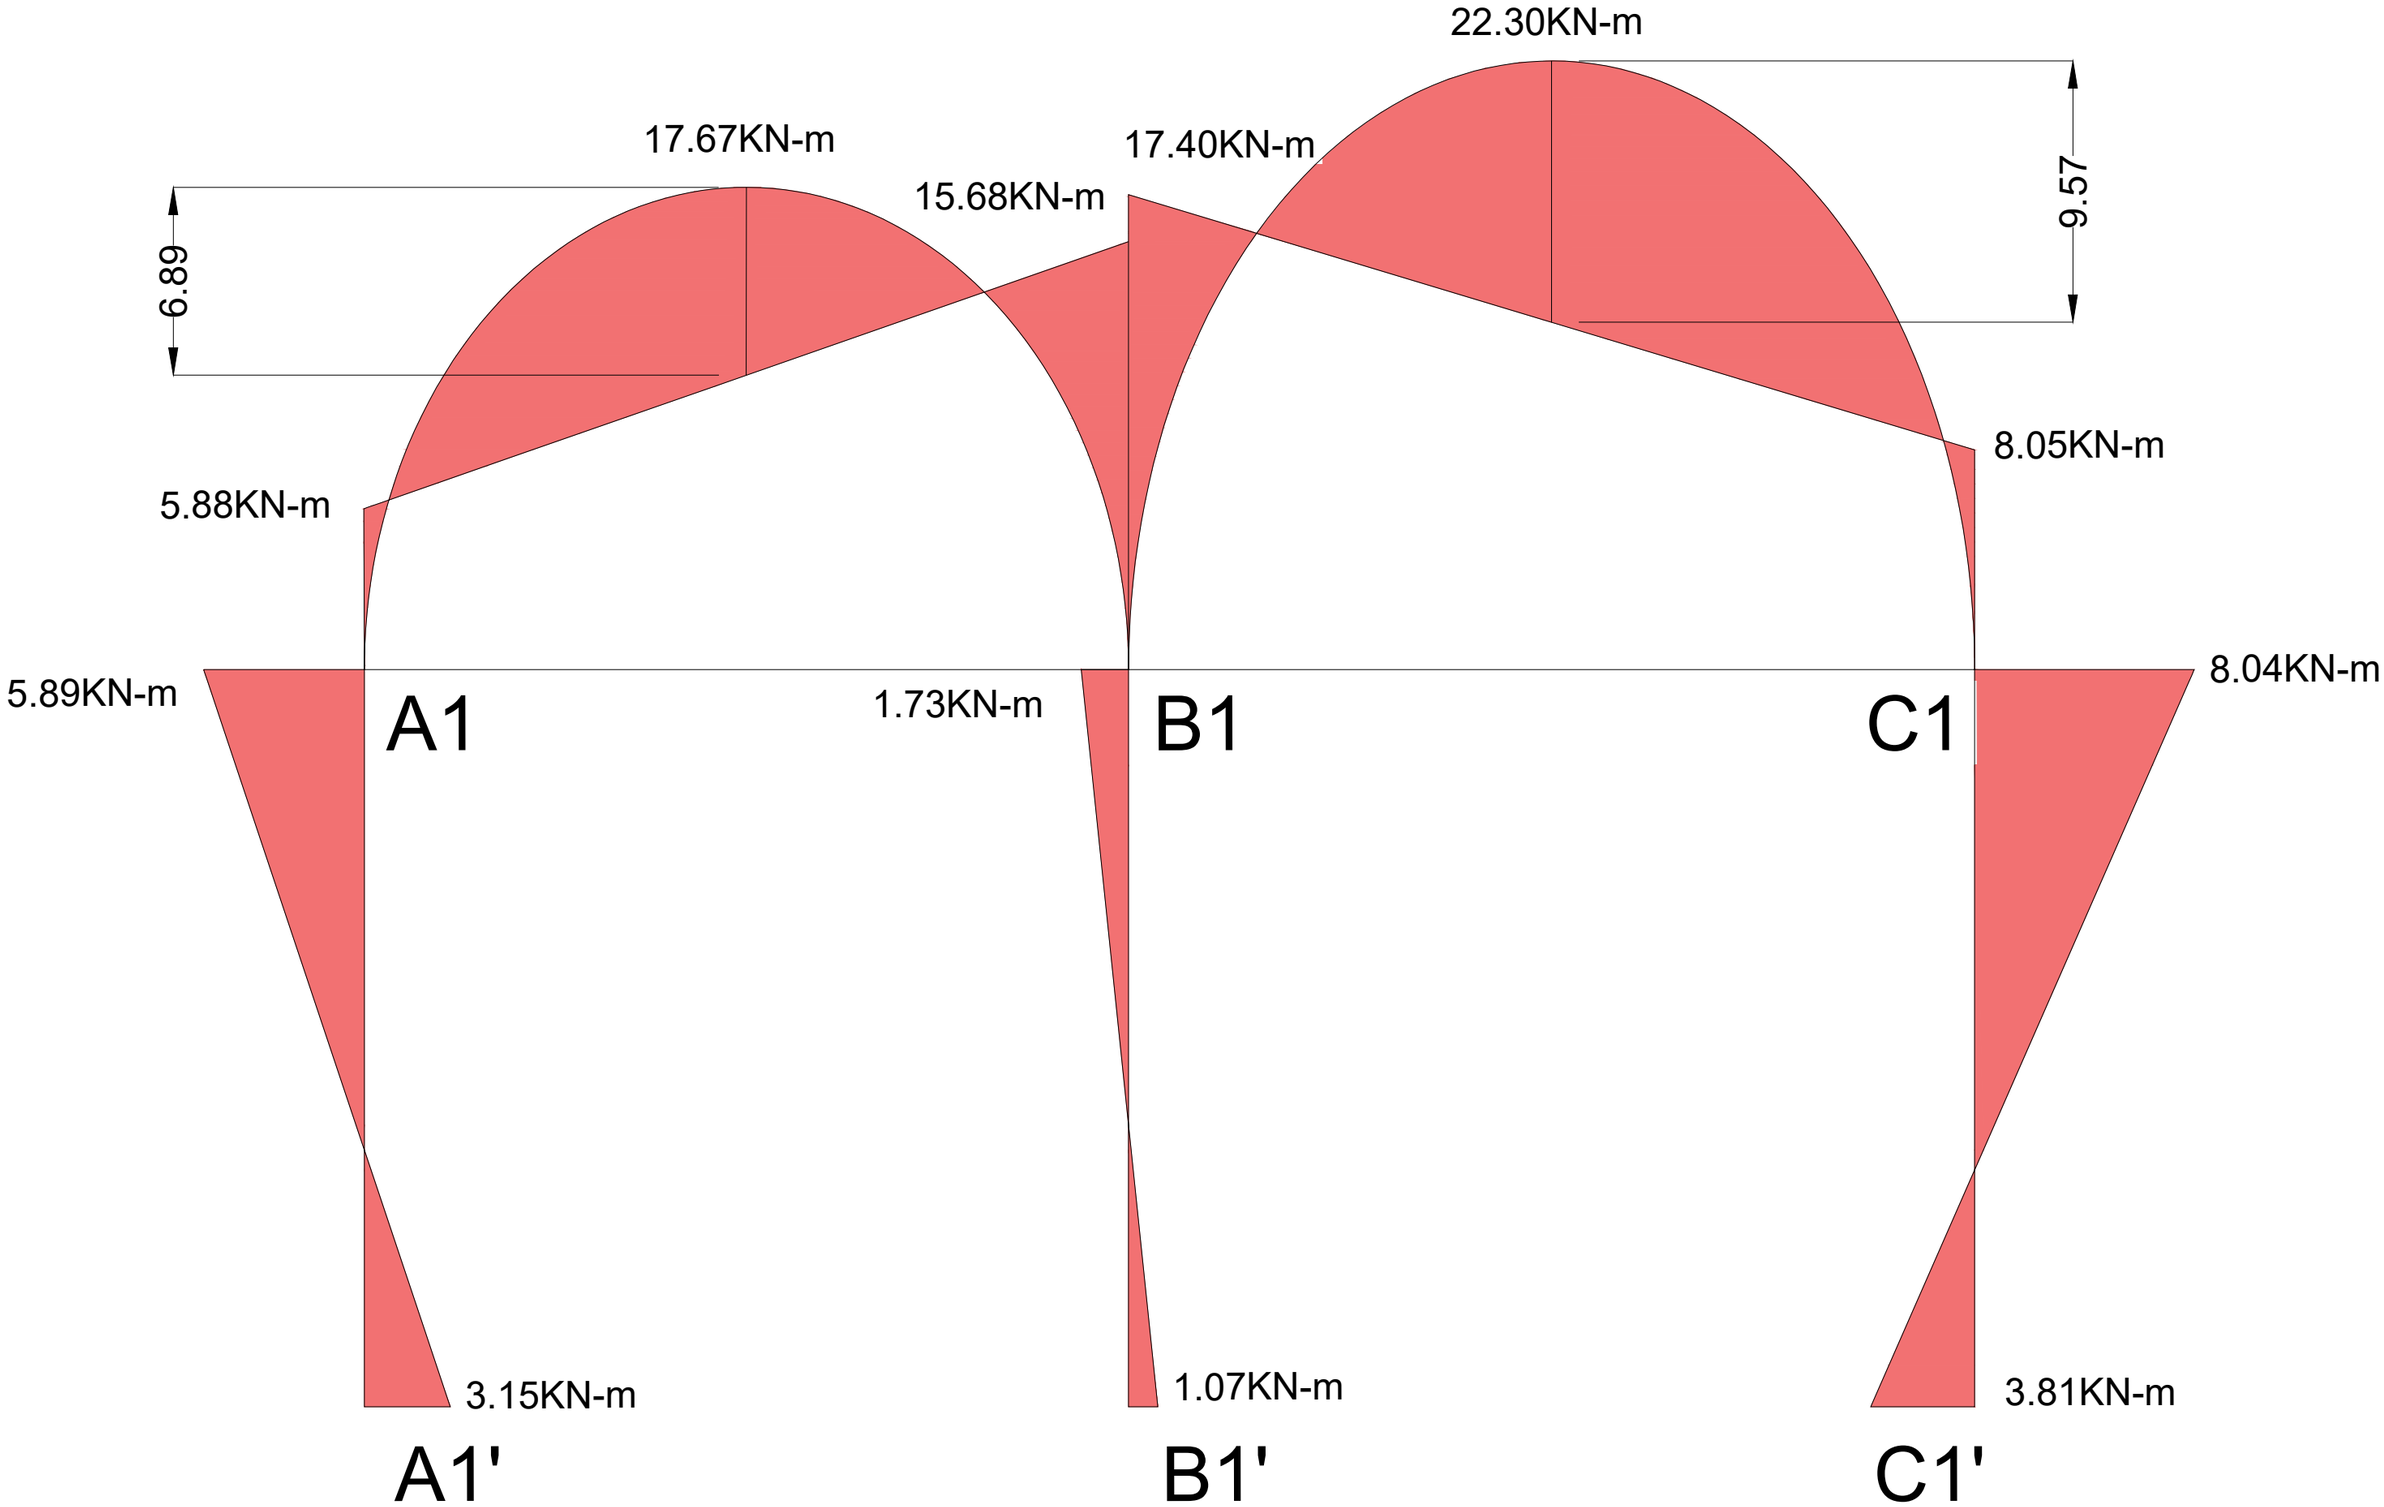

22.30KN-m
17.67KN-m
17.40KN-m
15.68KN-m
9.57
6.89
8.05KN-m
5.88KN-m
5.89KN-m
A1
1.73KN-m
B1
C1
8.04KN-m
3.15KN-m
1.07KN-m
3.81KN-m
A1'
B1'
C1'