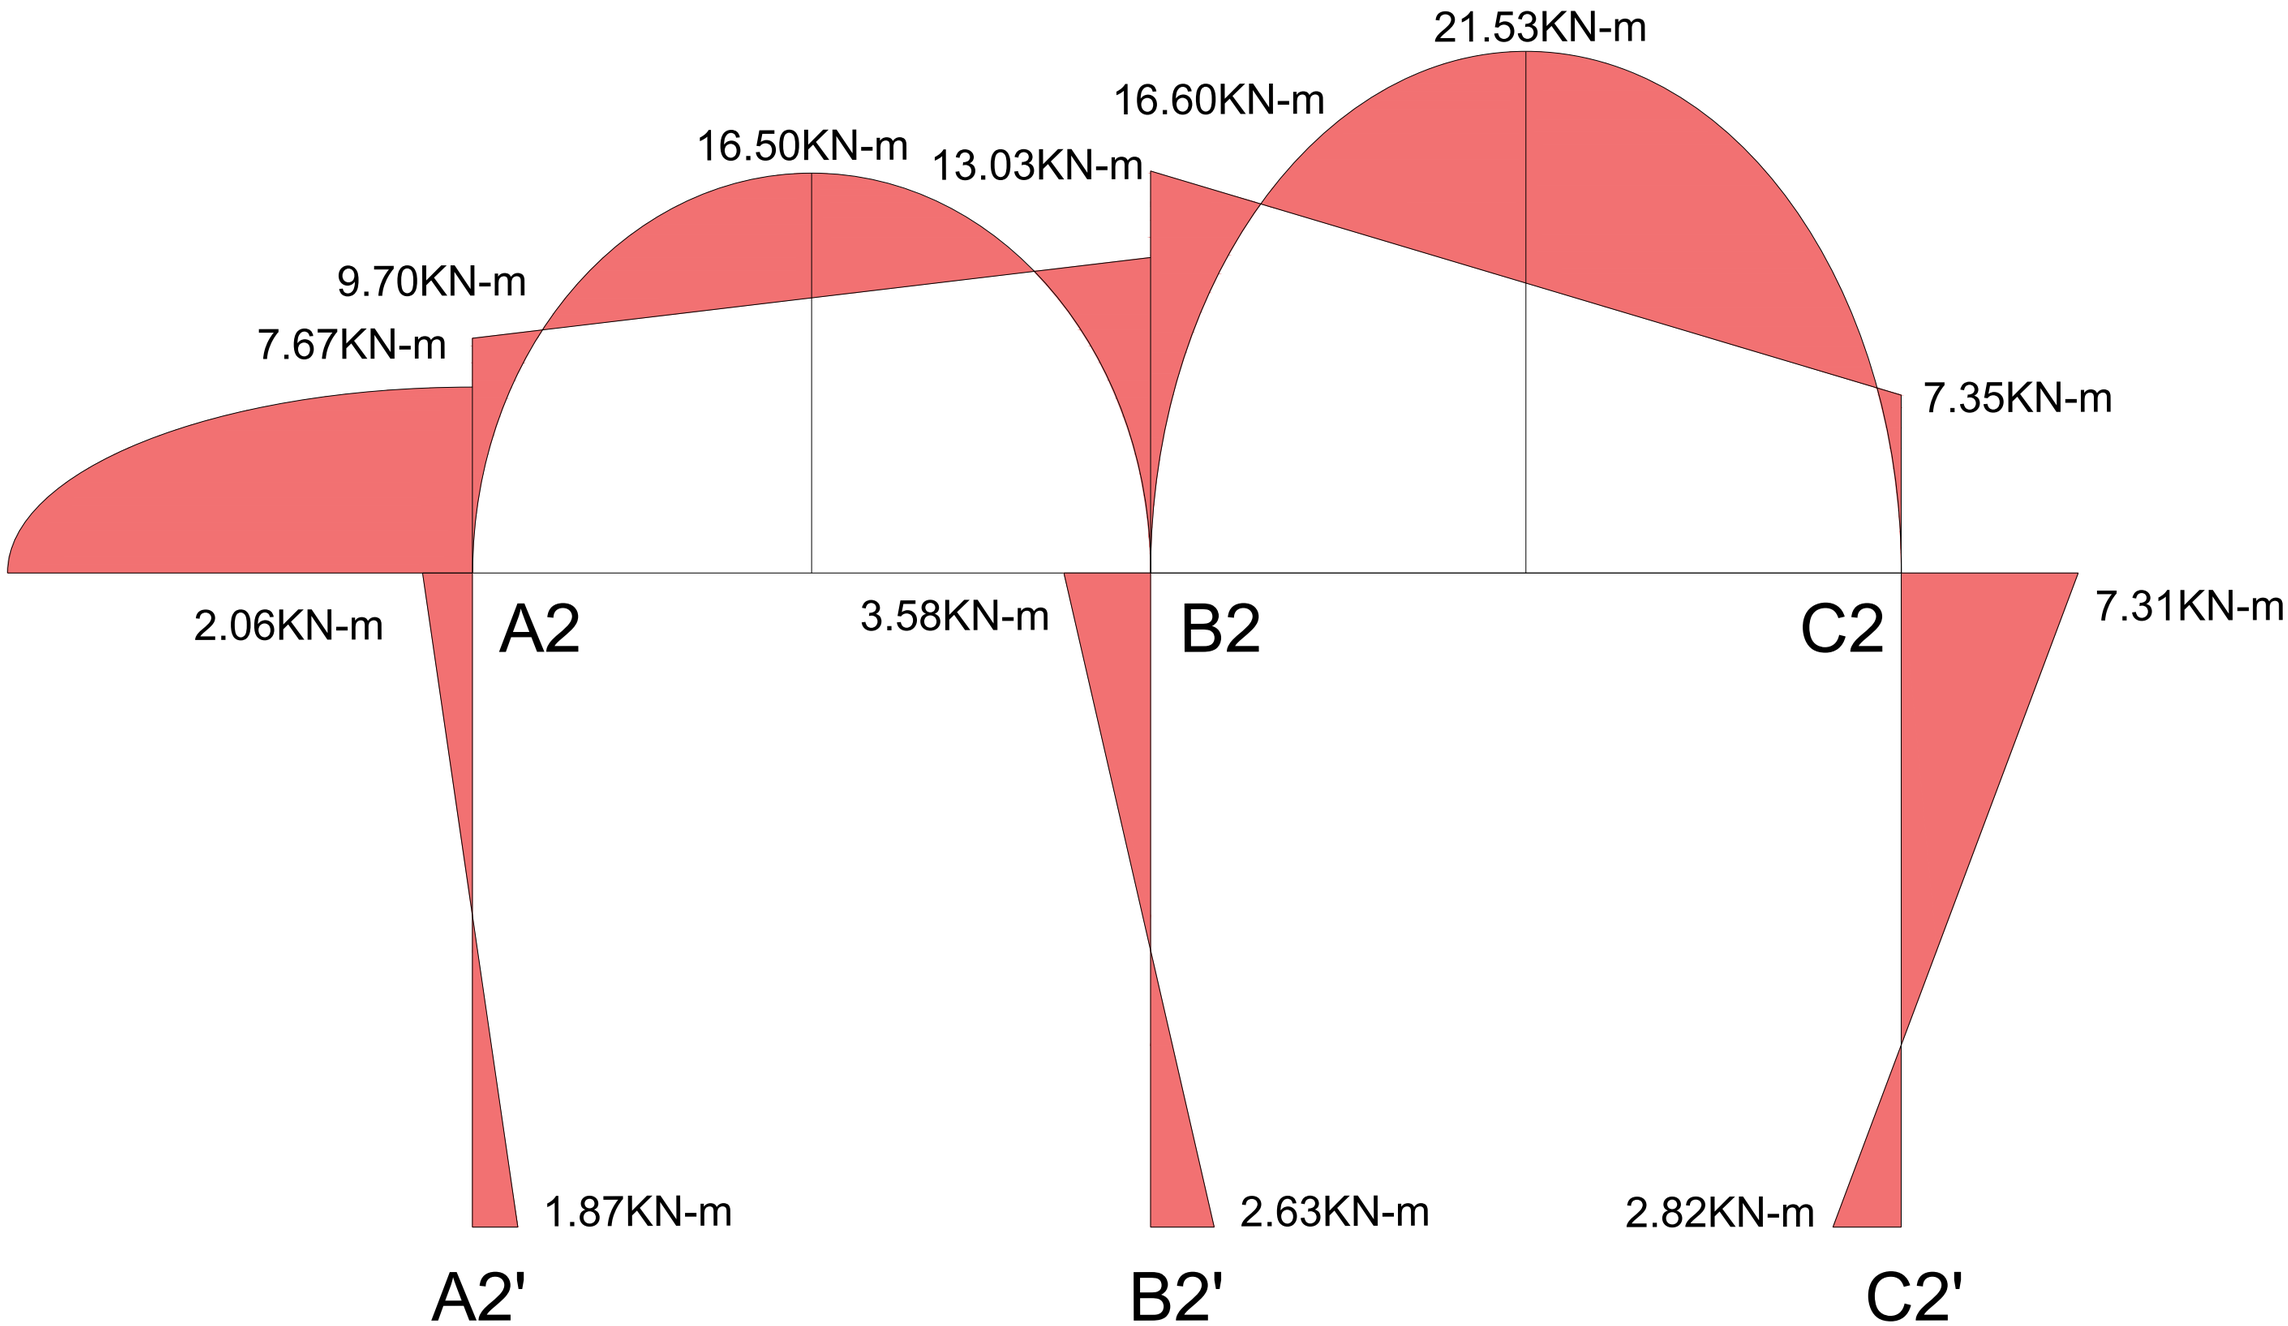

21.53KN-m
16.60KN-m
16.50KN-m
13.03KN-m
9.70KN-m
7.67KN-m
7.35KN-m
2.06KN-m
A2
3.58KN-m
B2
C2
7.31KN-m
1.87KN-m
2.63KN-m
2.82KN-m
A2'
B2'
C2'