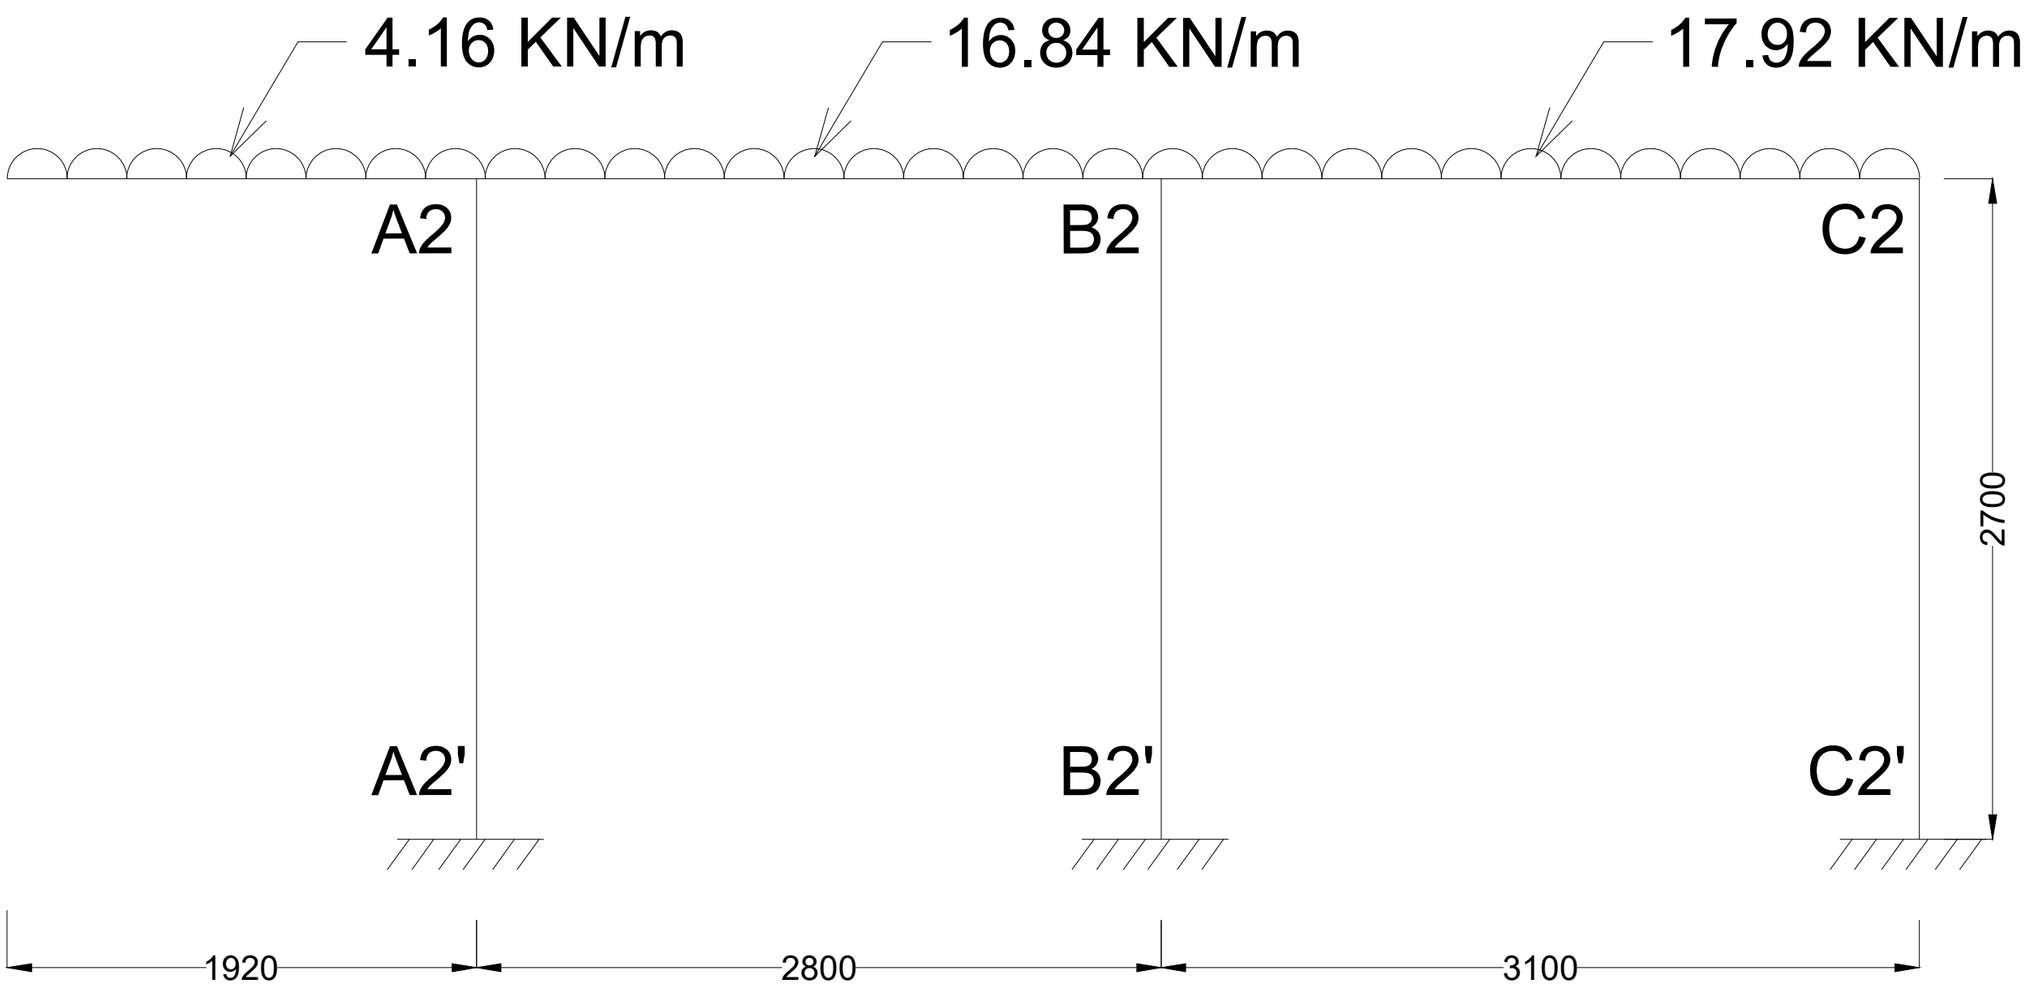

4.16 KN/m
16.84 KN/m
17.92 KN/m
A2
B2
C2
2700
A2'
B2'
C2'
1920
2800
3100