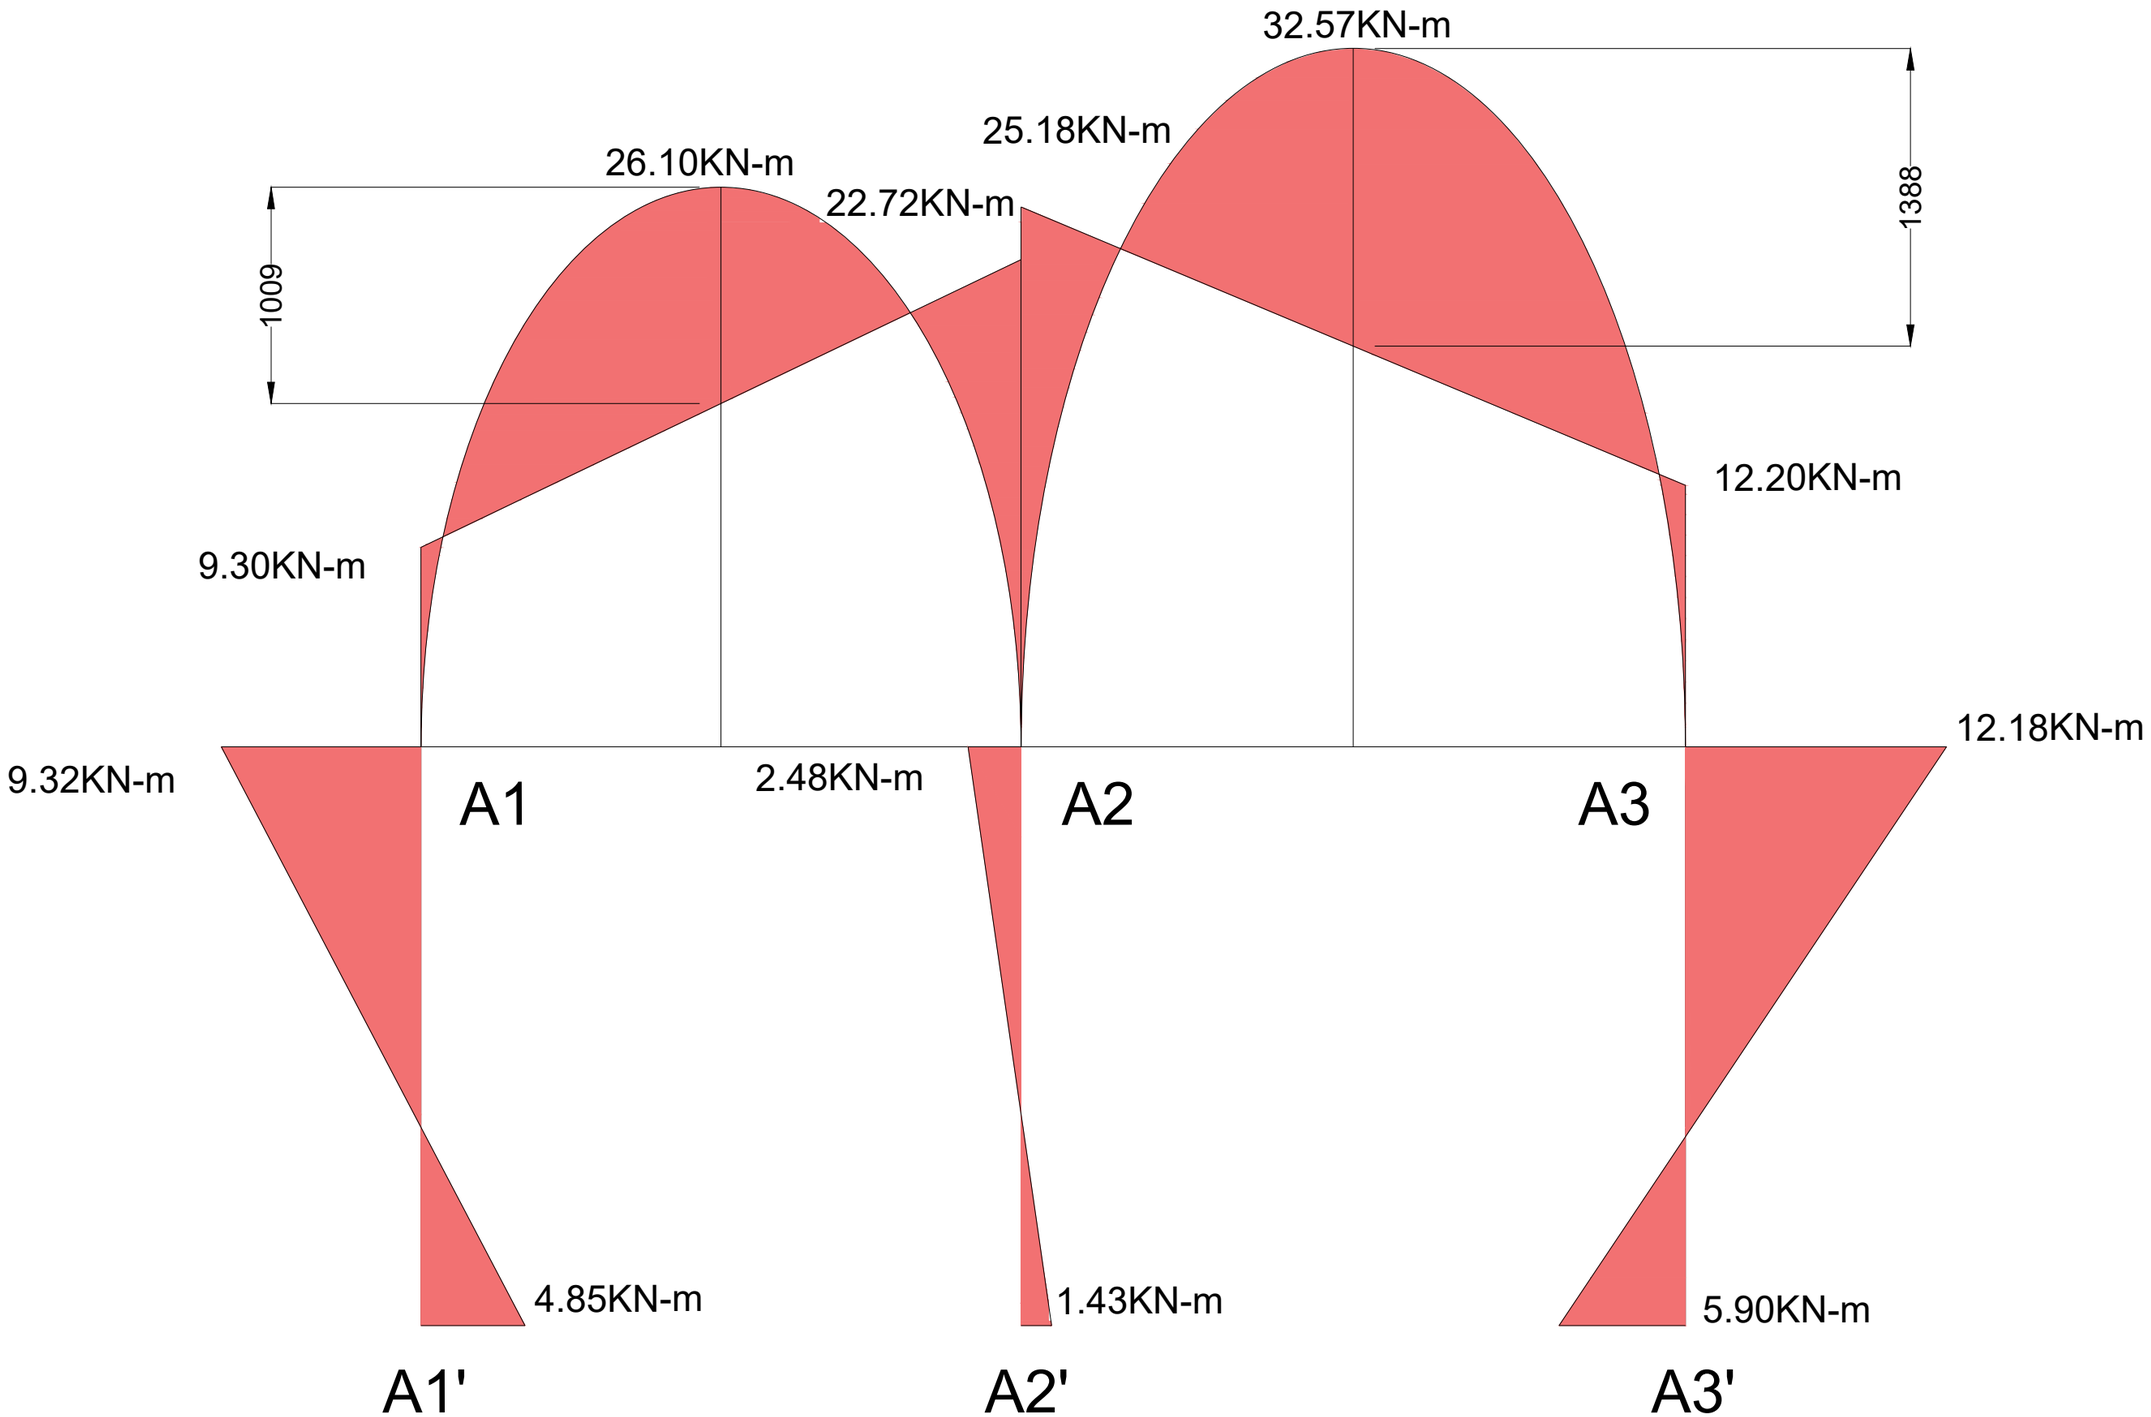

32.57KN-m
25.18KN-m
26.10KN-m
22.72KN-m
1388
1009
12.20KN-m
9.30KN-m
12.18KN-m
9.32KN-m
2.48KN-m
A1
A2
A3
4.85KN-m
1.43KN-m
5.90KN-m
A1'
A2'
A3'