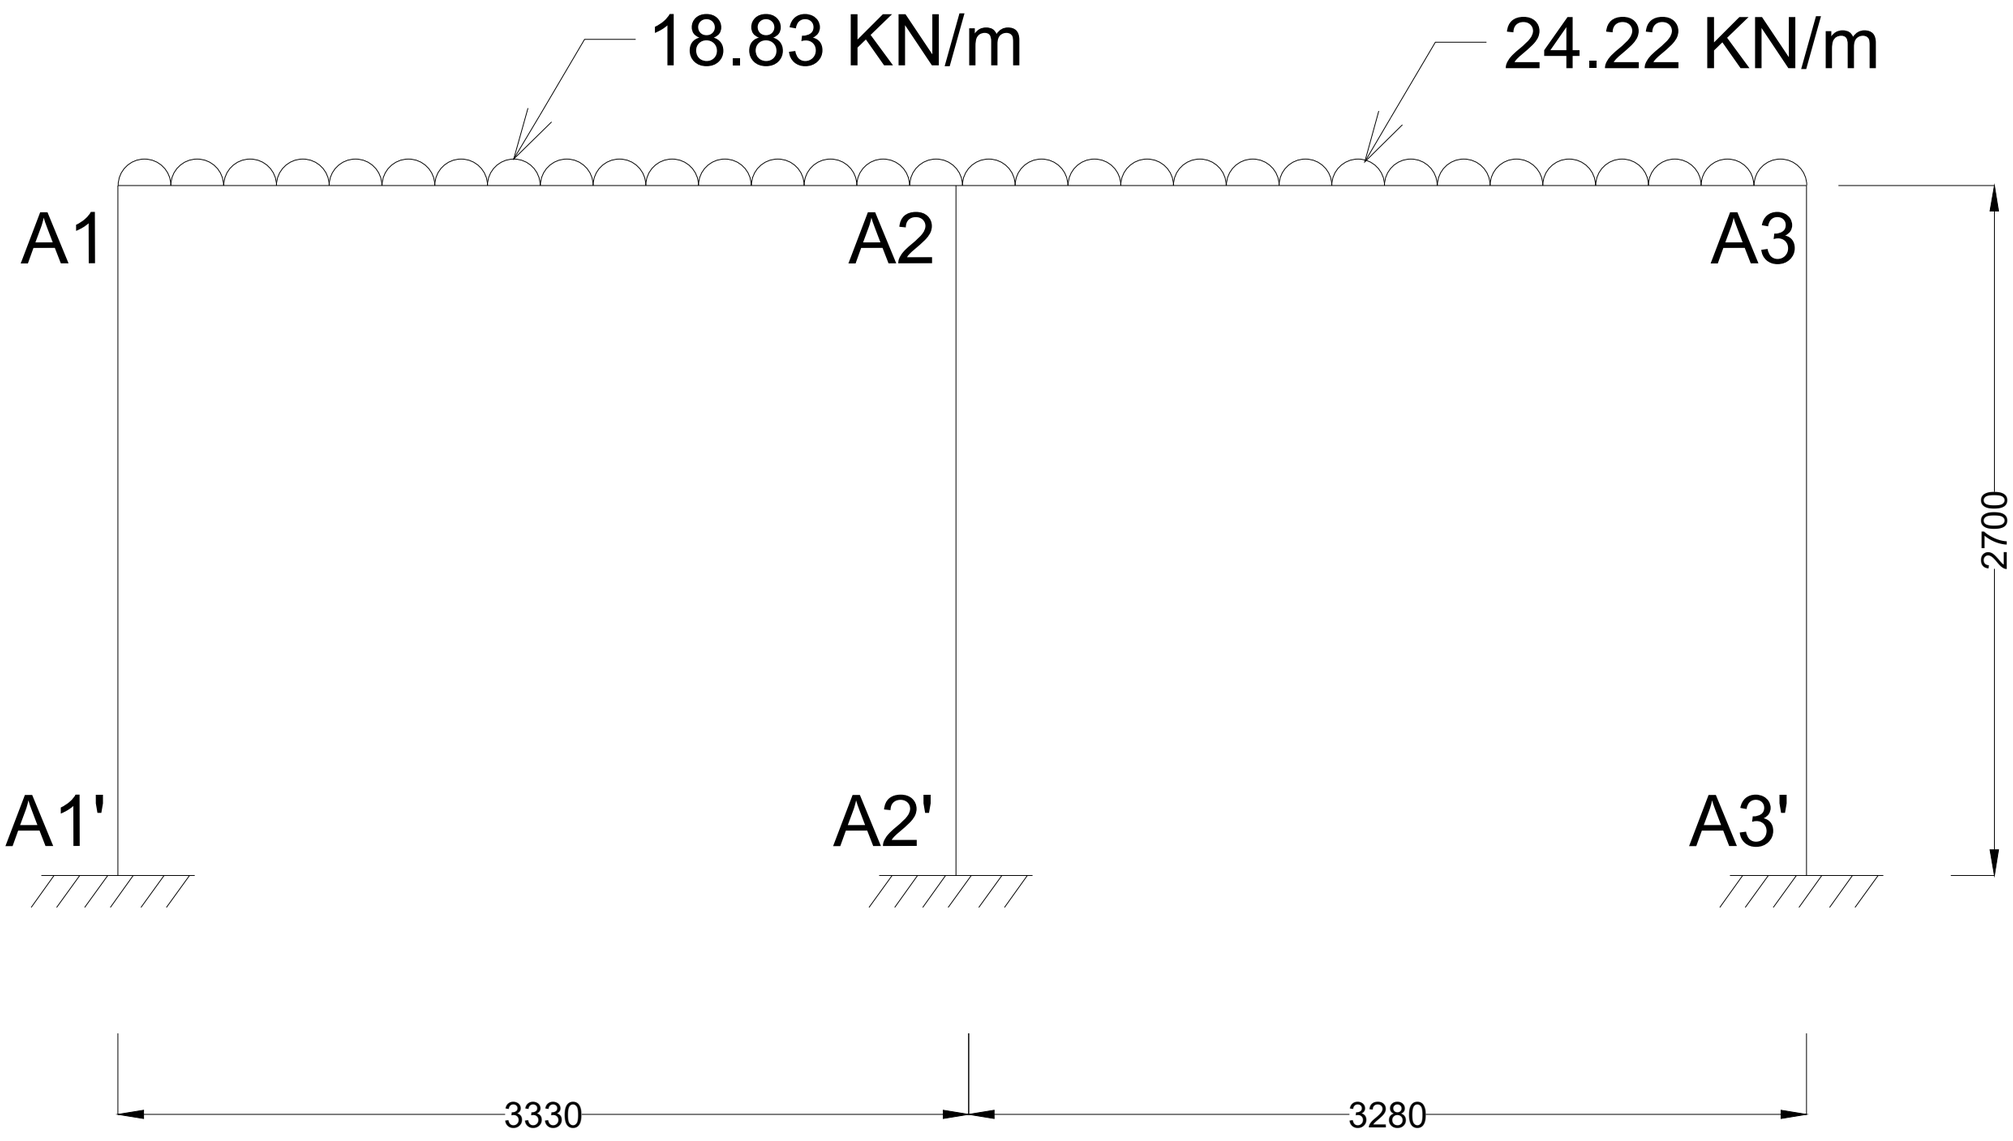

18.83 KN/m
24.22 KN/m
A1
A2
A3
A1'
A2'
A3'
2700
3330
3280