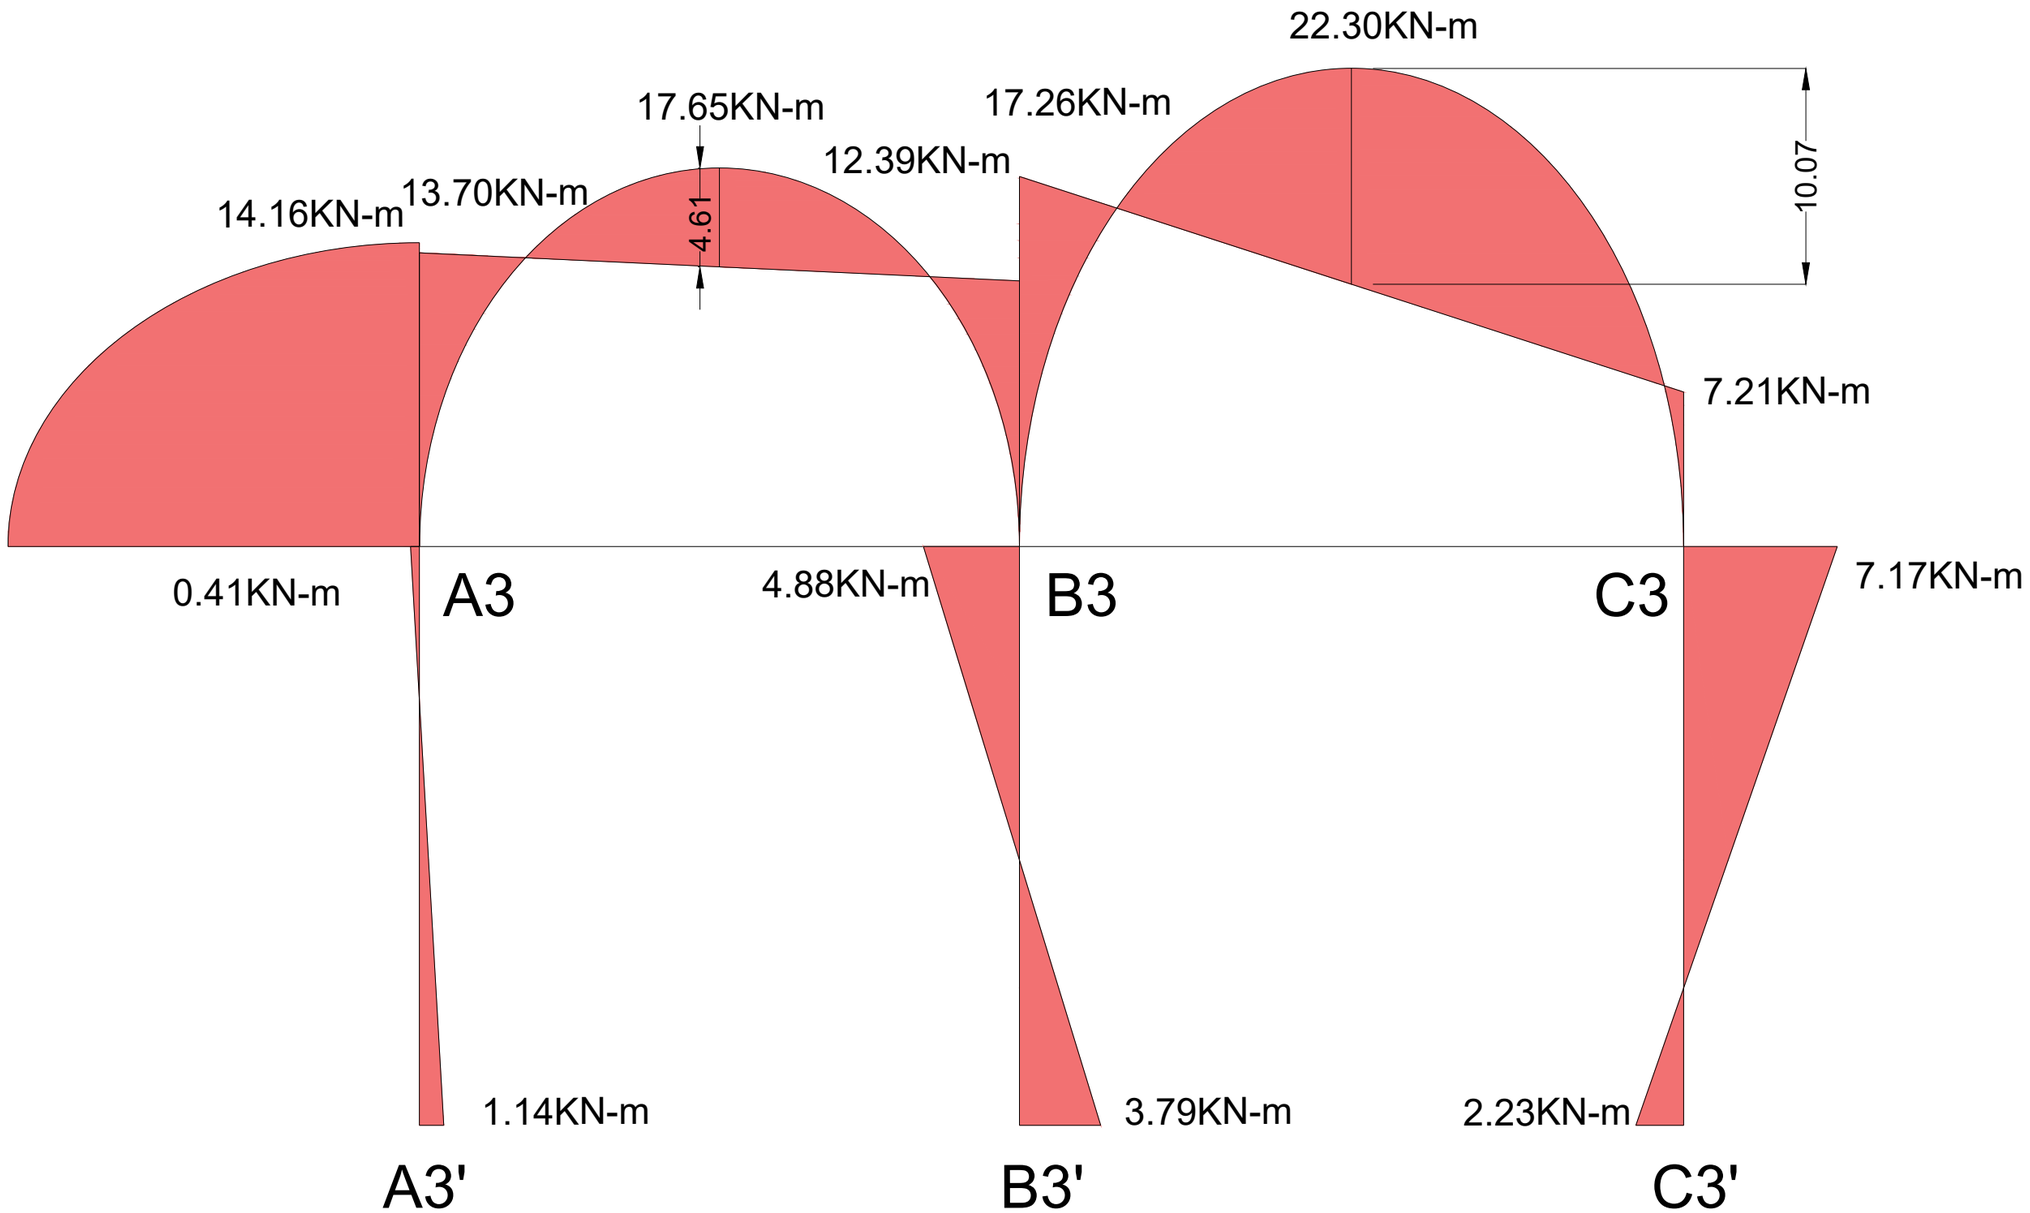

22.30KN-m
17.65KN-m
17.26KN-m
12.39KN-m
14.16KN-m
13.70KN-m
4.61
10.07
7.21KN-m
0.41KN-m
A3
4.88KN-m
B3
C3
7.17KN-m
1.14KN-m
3.79KN-m
2.23KN-m
A3'
B3'
C3'