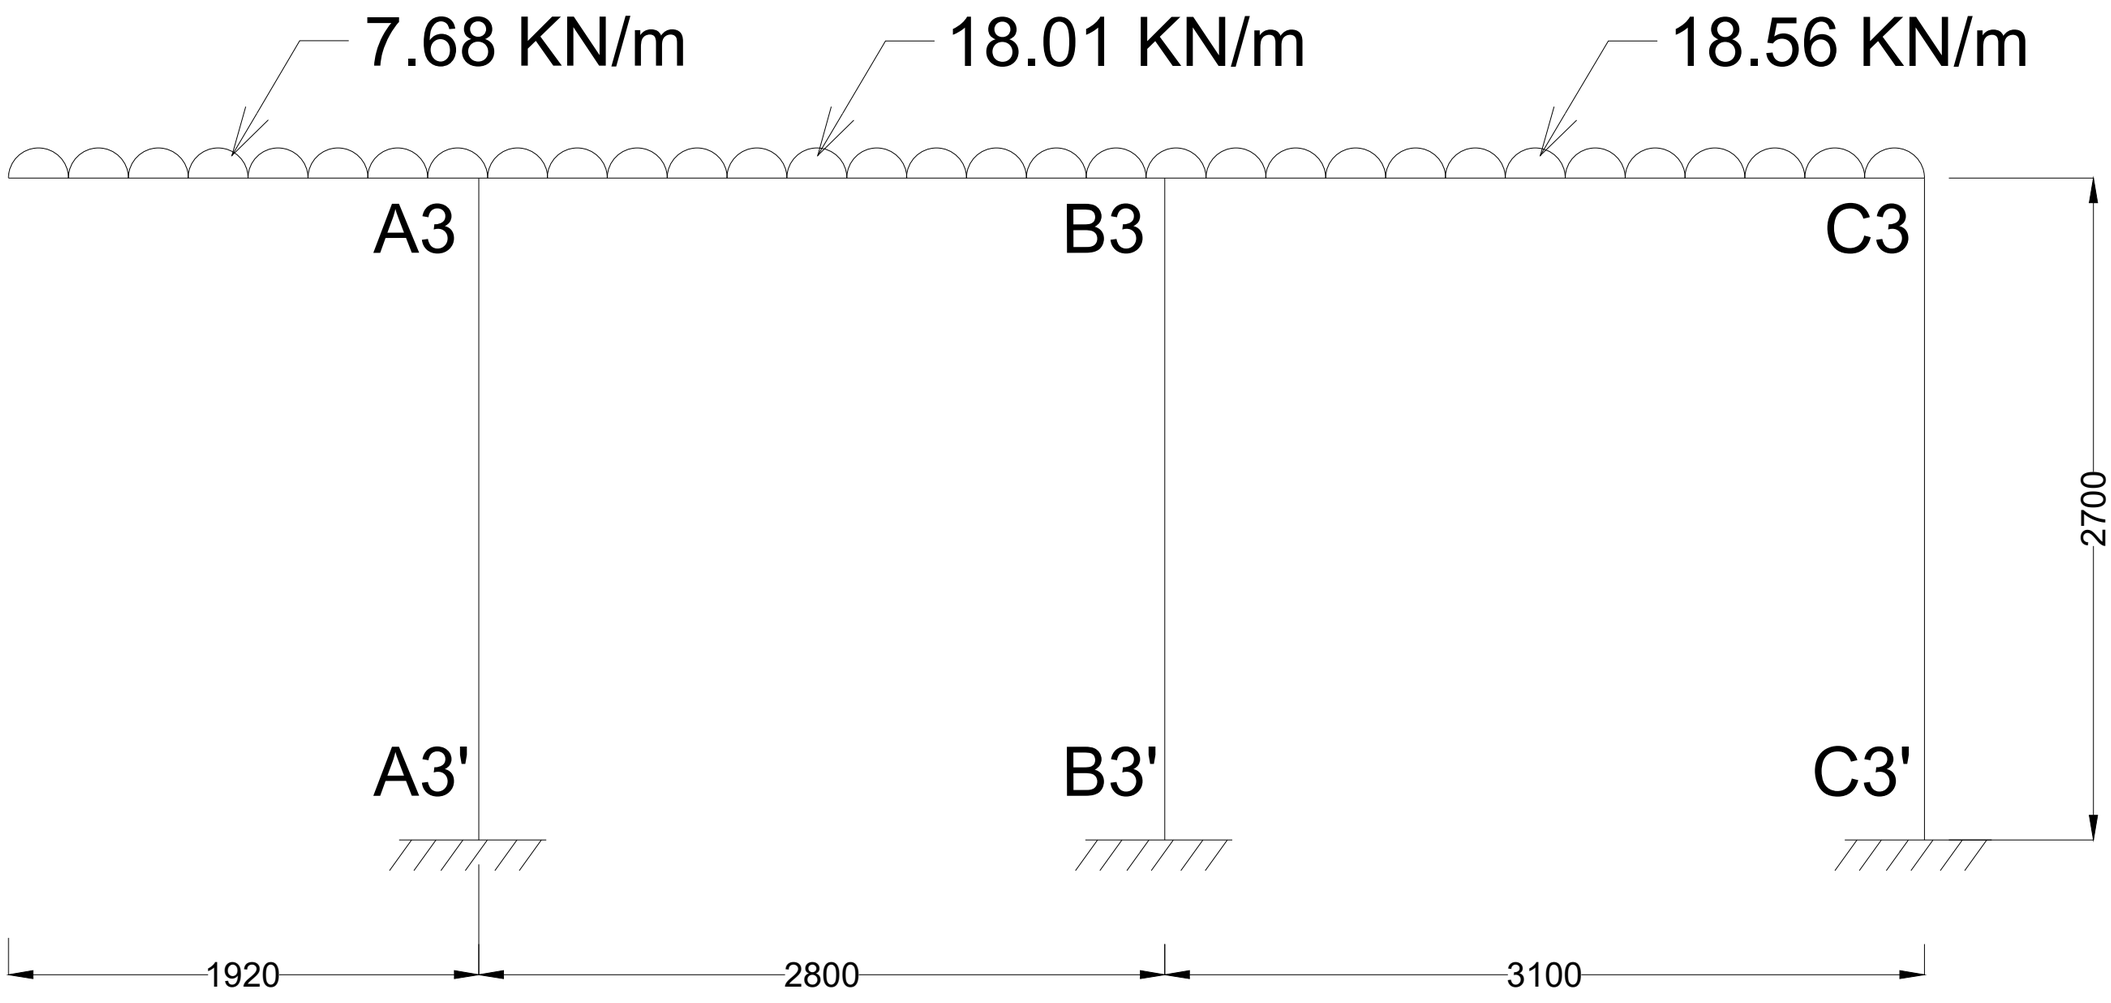

7.68 KN/m
18.01 KN/m
18.56 KN/m
A3
B3
C3
2700
A3'
B3'
C3'
1920
2800
3100