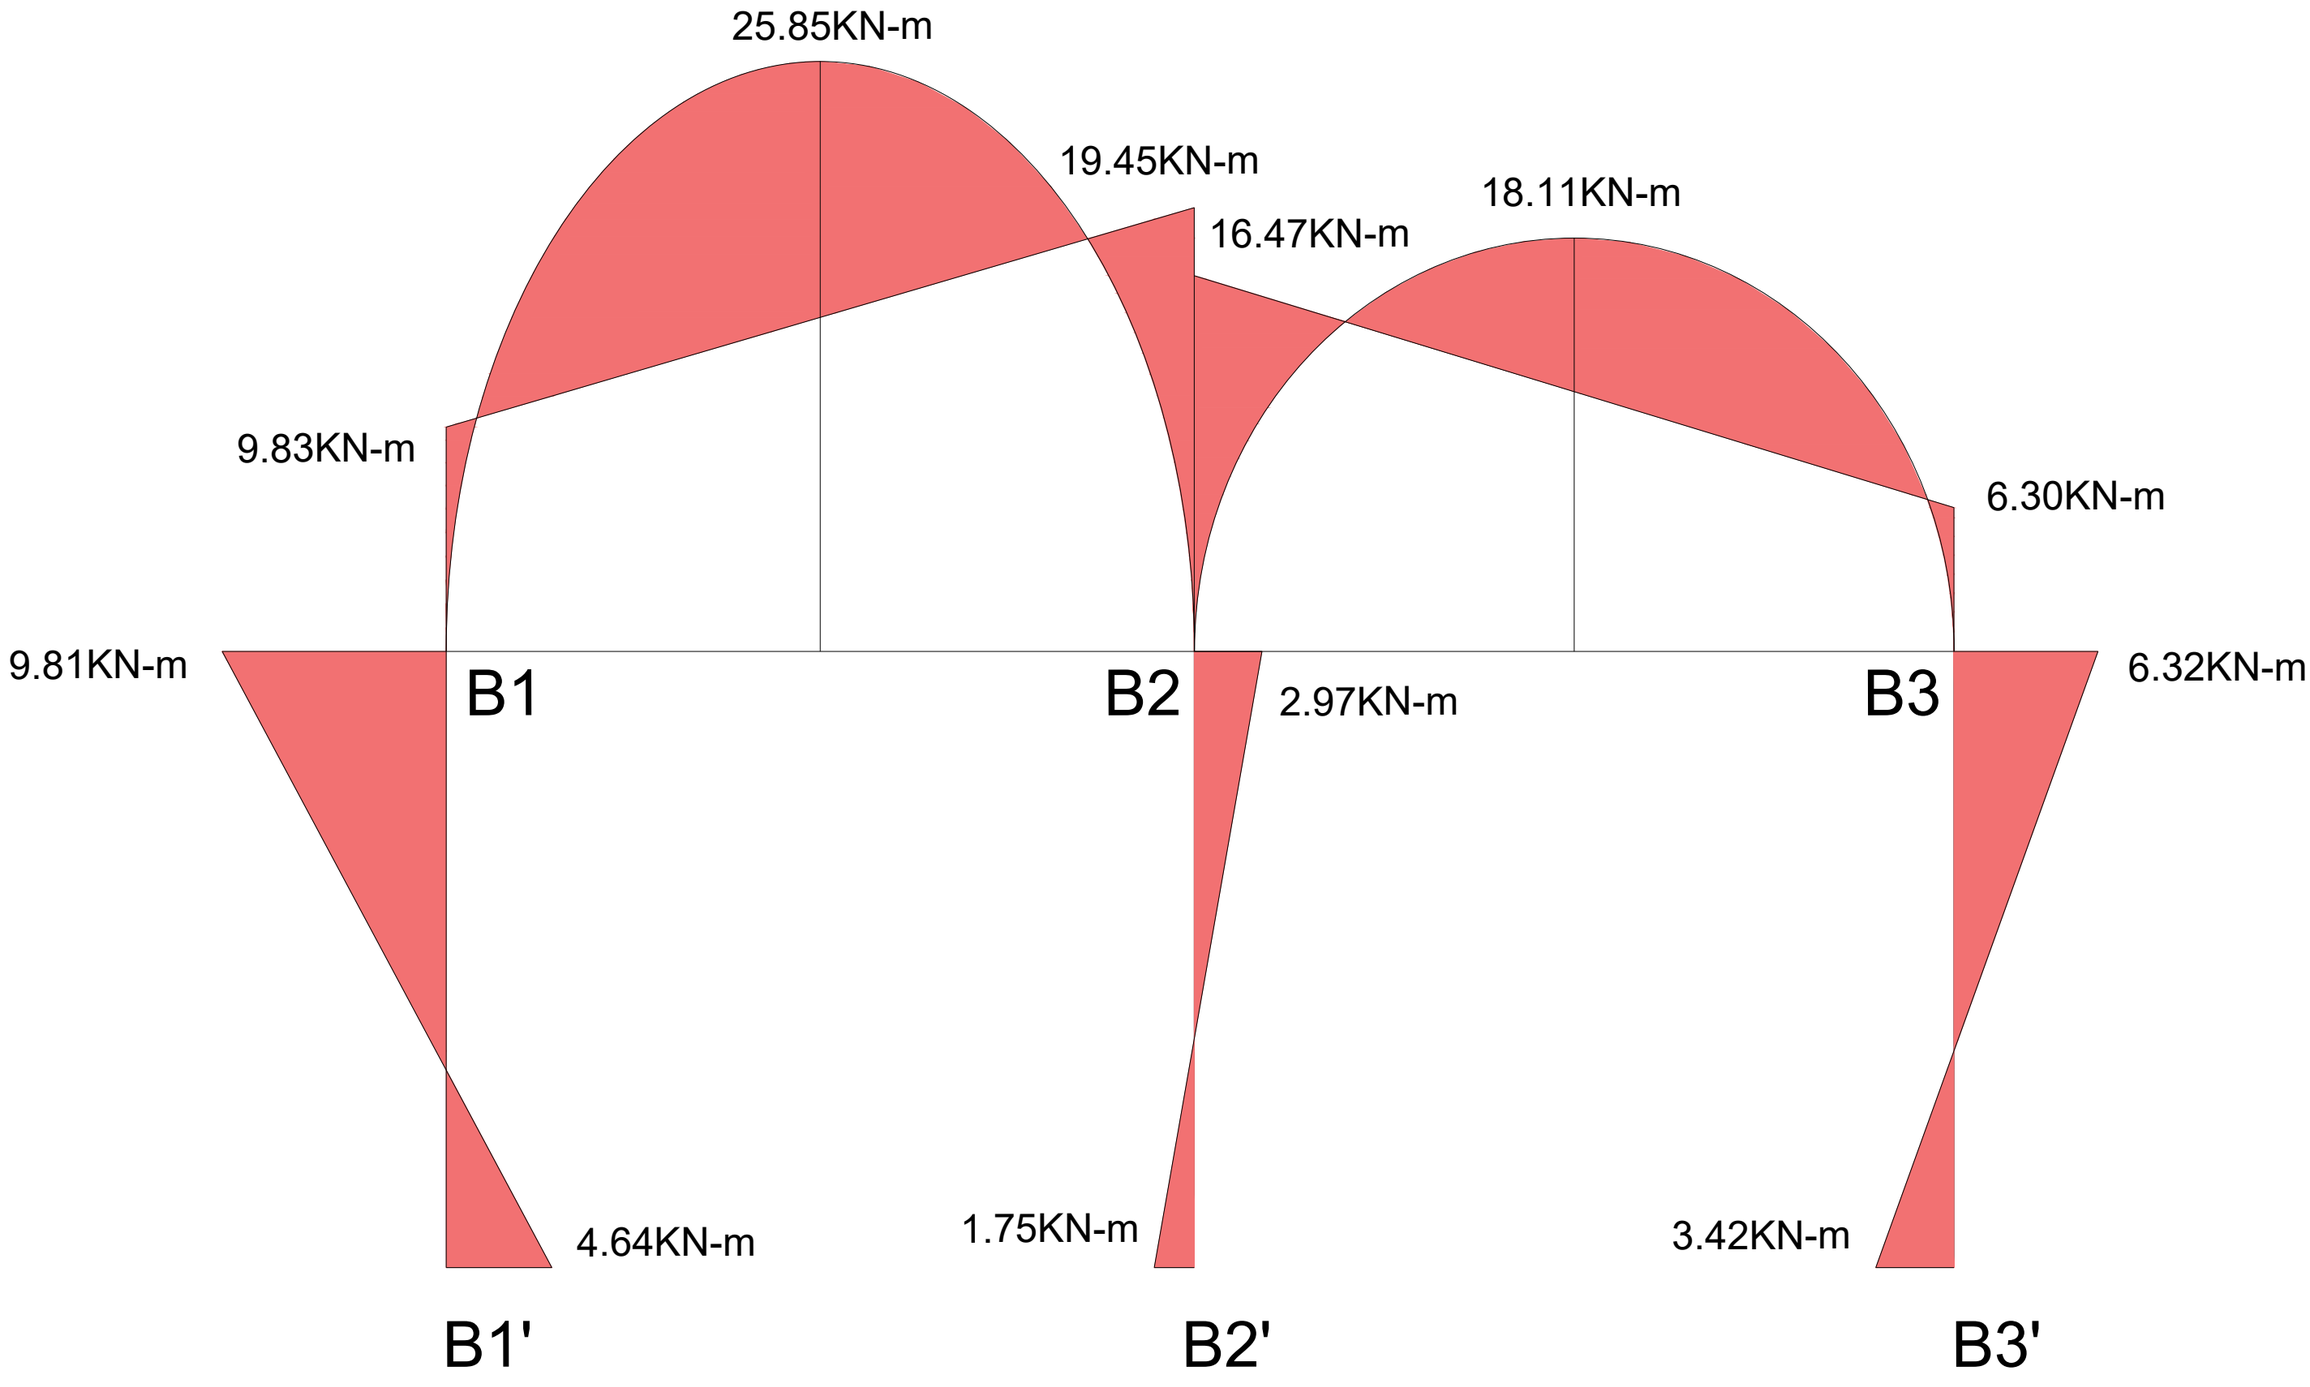

25.85KN-m
19.45KN-m
16.47KN-m
18.11KN-m
9.83KN-m
6.30KN-m
9.81KN-m
6.32KN-m
B1
B2
B3
2.97KN-m
4.64KN-m
1.75KN-m
3.42KN-m
B1'
B2'
B3'