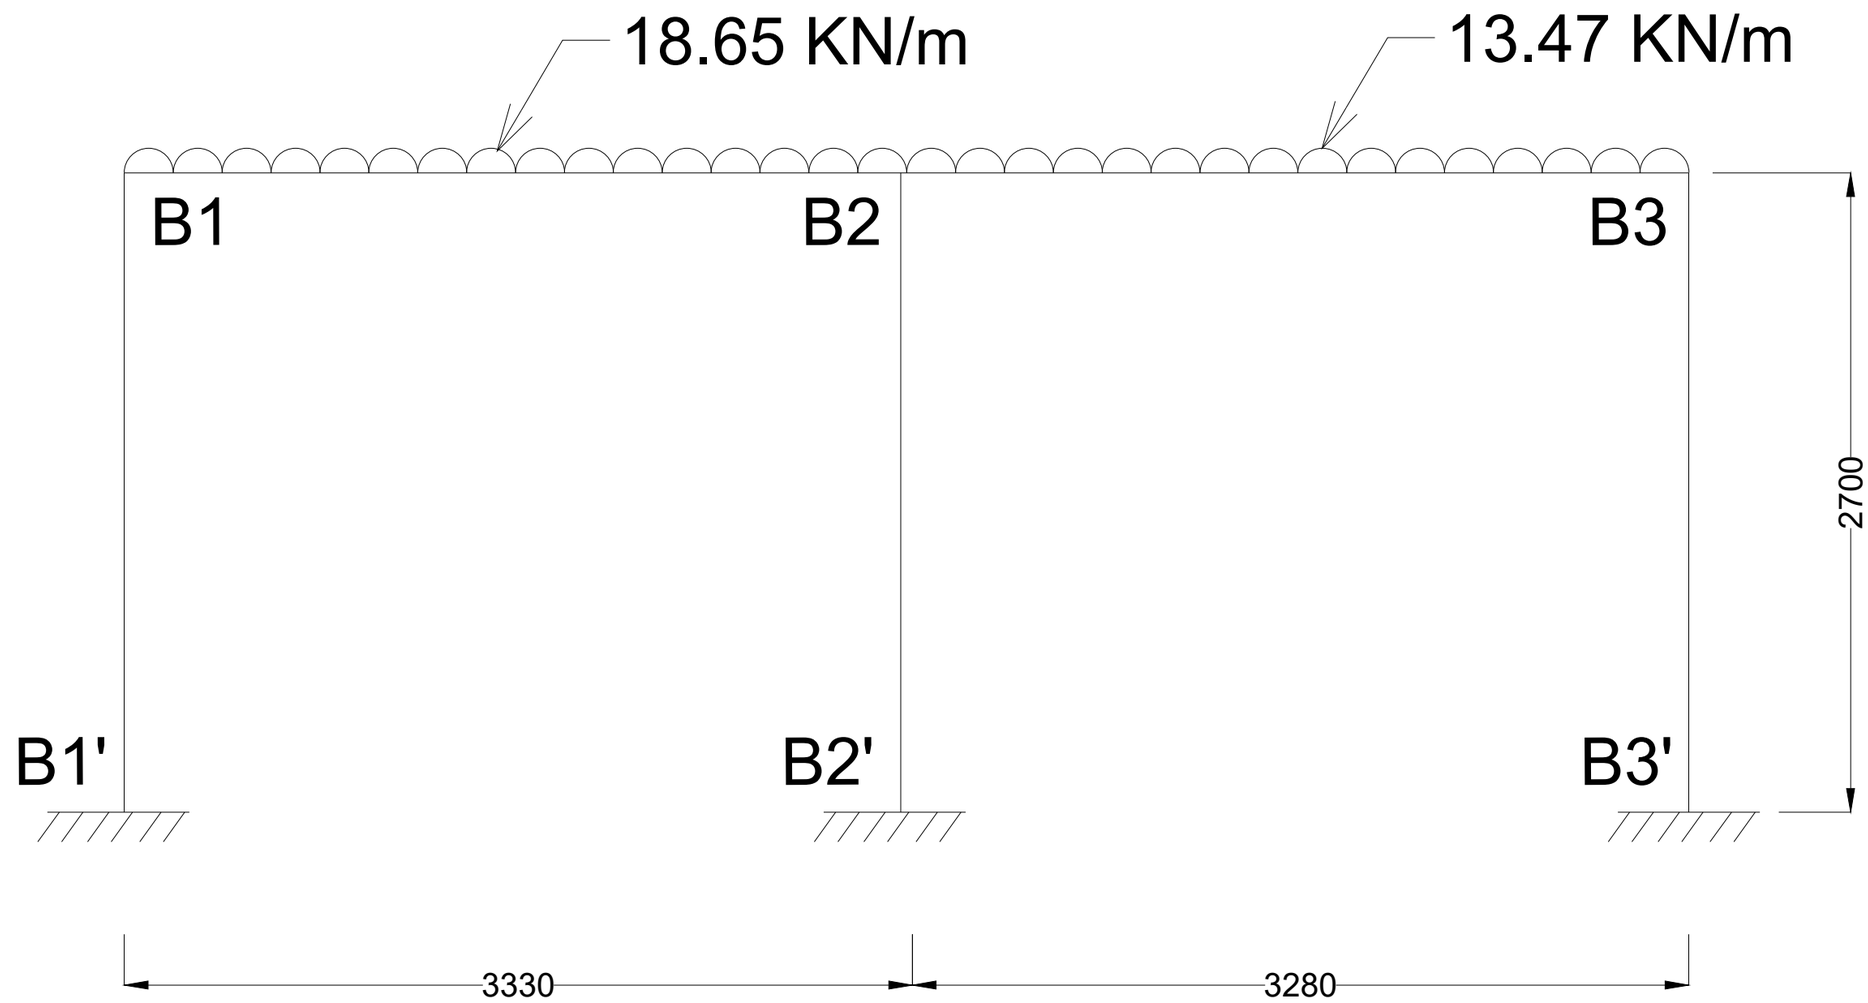

18.65 KN/m
13.47 KN/m
B1
B2
B3
2700
B1'
B2'
B3'
3330
3280