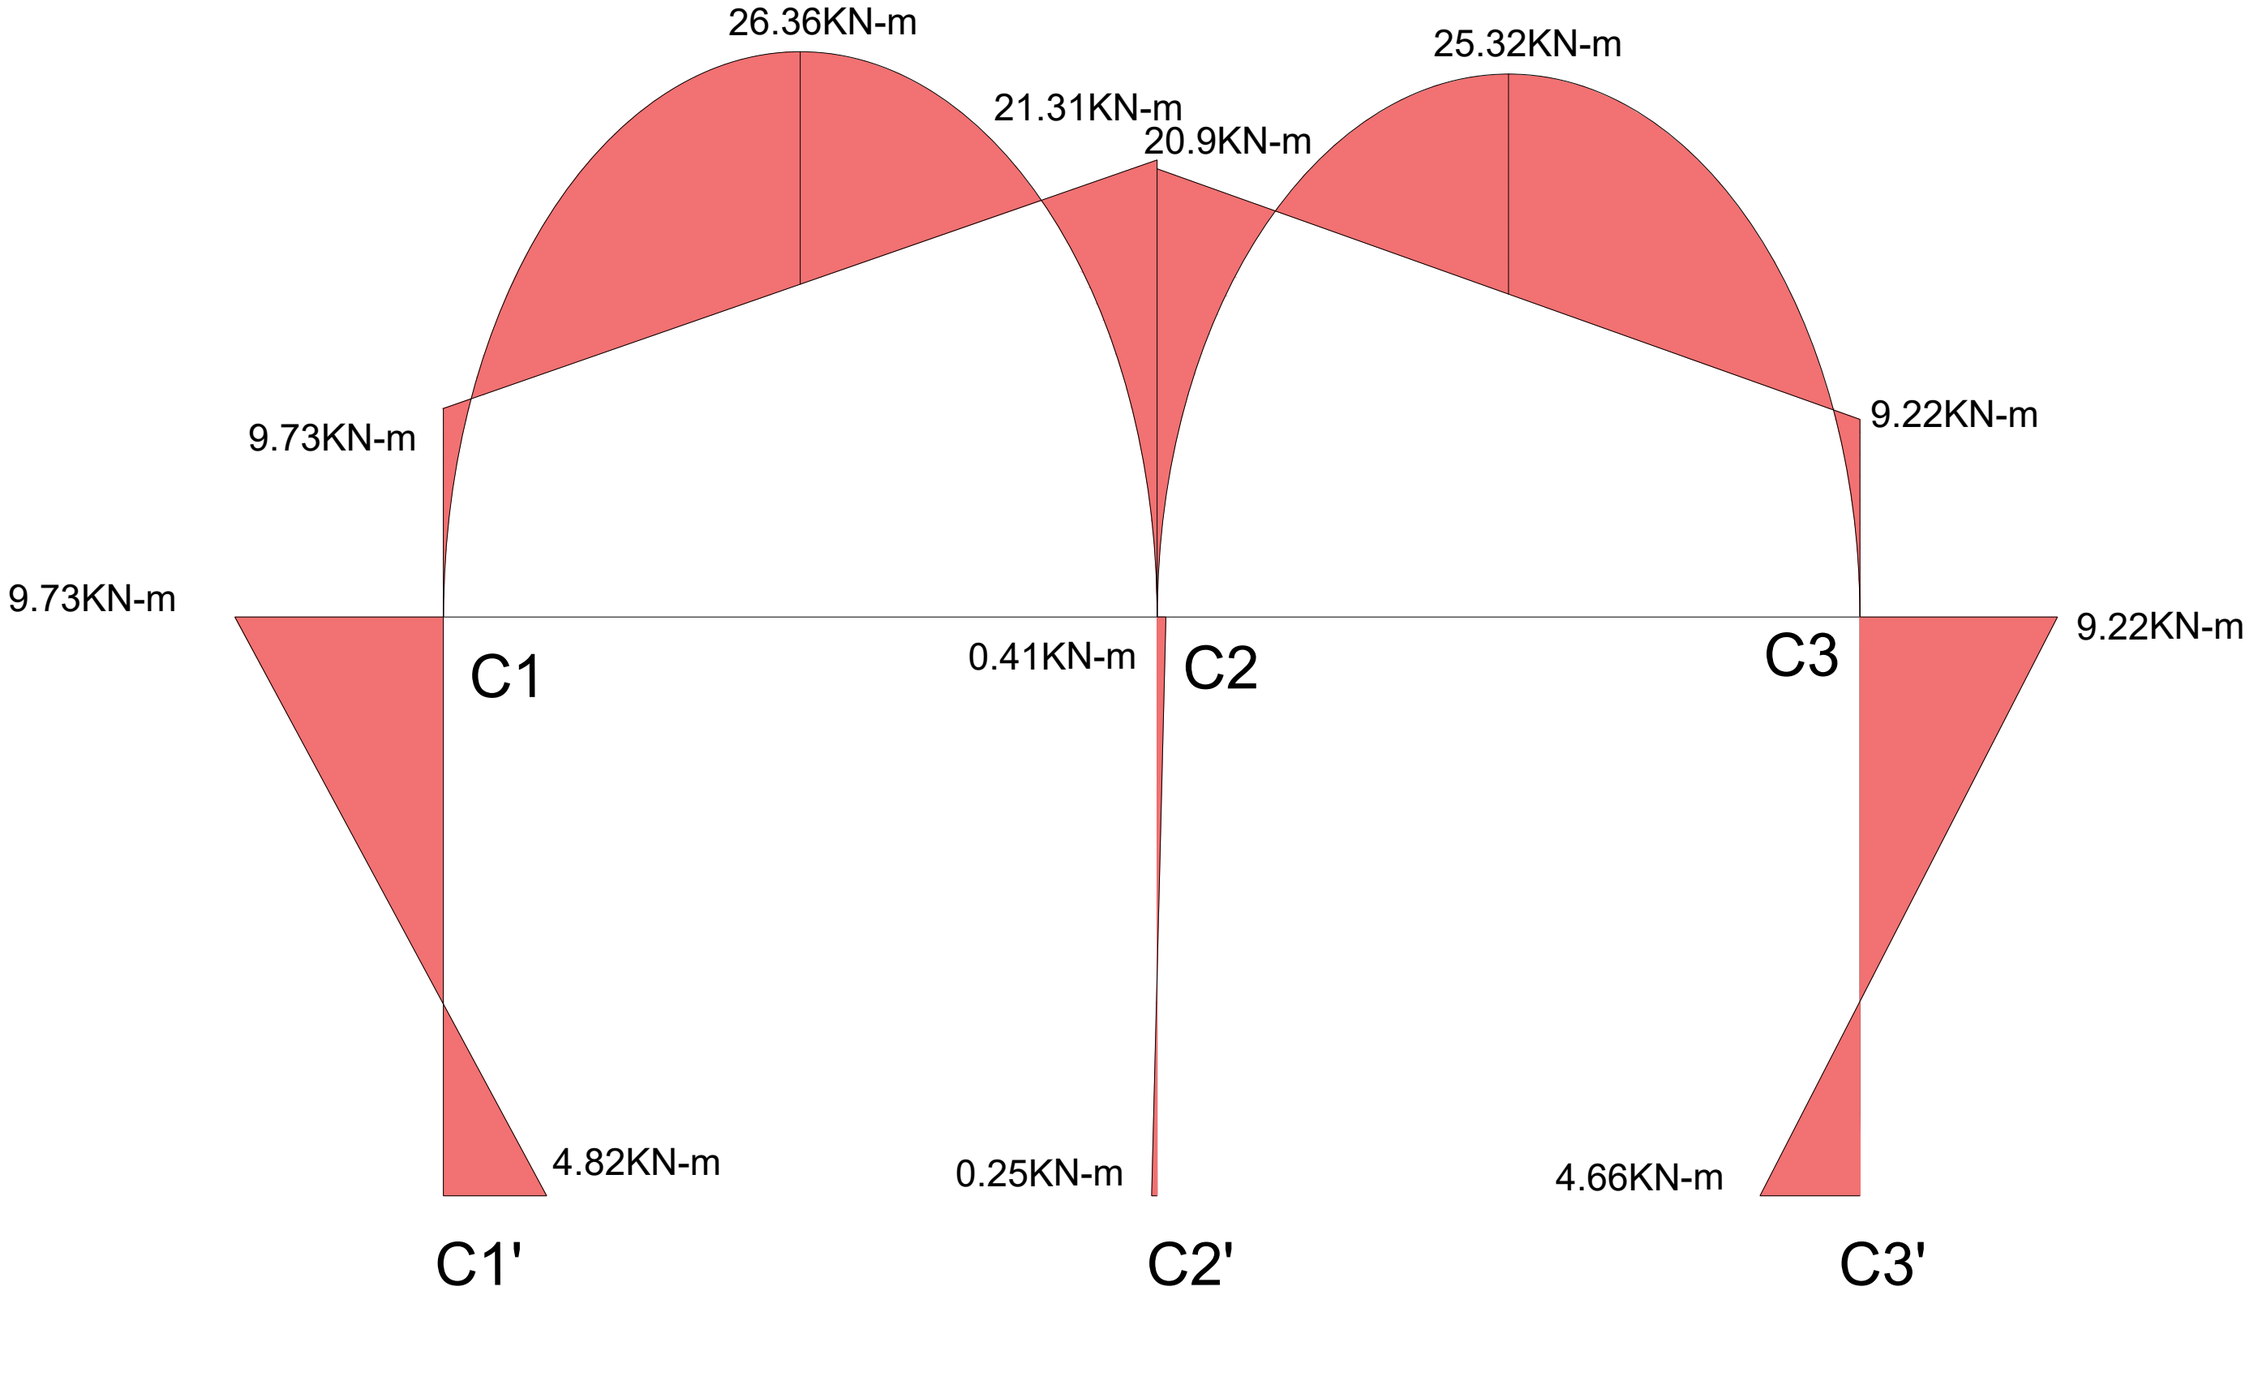

26.36KN-m
25.32KN-m
21.31KN-m
20.9KN-m
9.73KN-m
9.22KN-m
9.73KN-m
9.22KN-m
C1
0.41KN-m
C2
C3
4.82KN-m
0.25KN-m
4.66KN-m
C1'
C2'
C3'