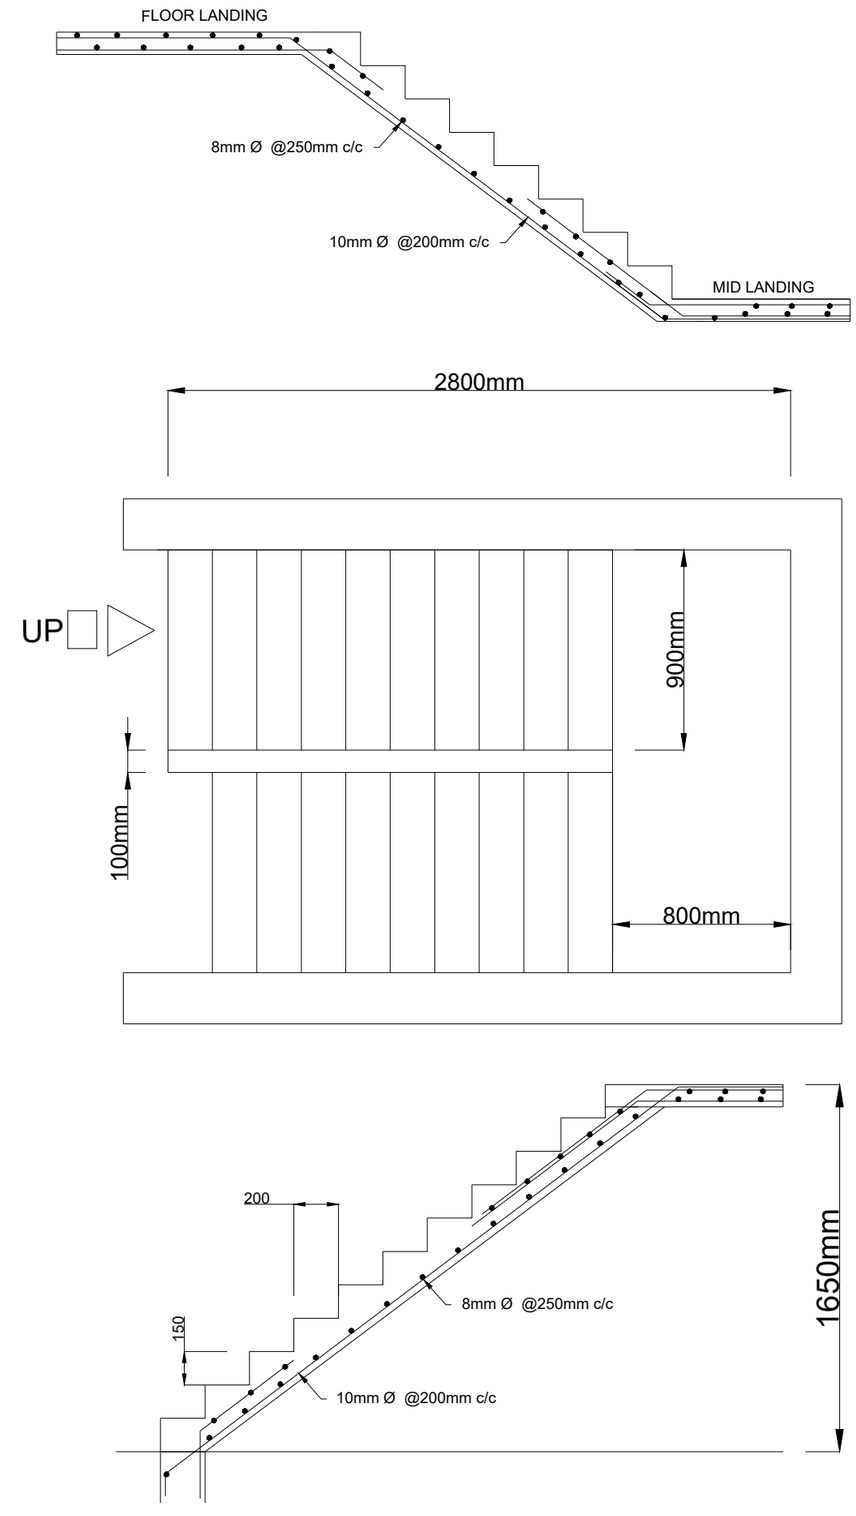

FLOOR LANDING
8mm Ø @250mm c/c
10mm Ø @200mm c/c
MID LANDING
2800mm
UP
900mm
100mm
800mm
200
150
8mm Ø @250mm c/c
10mm Ø @200mm c/c
1650mm