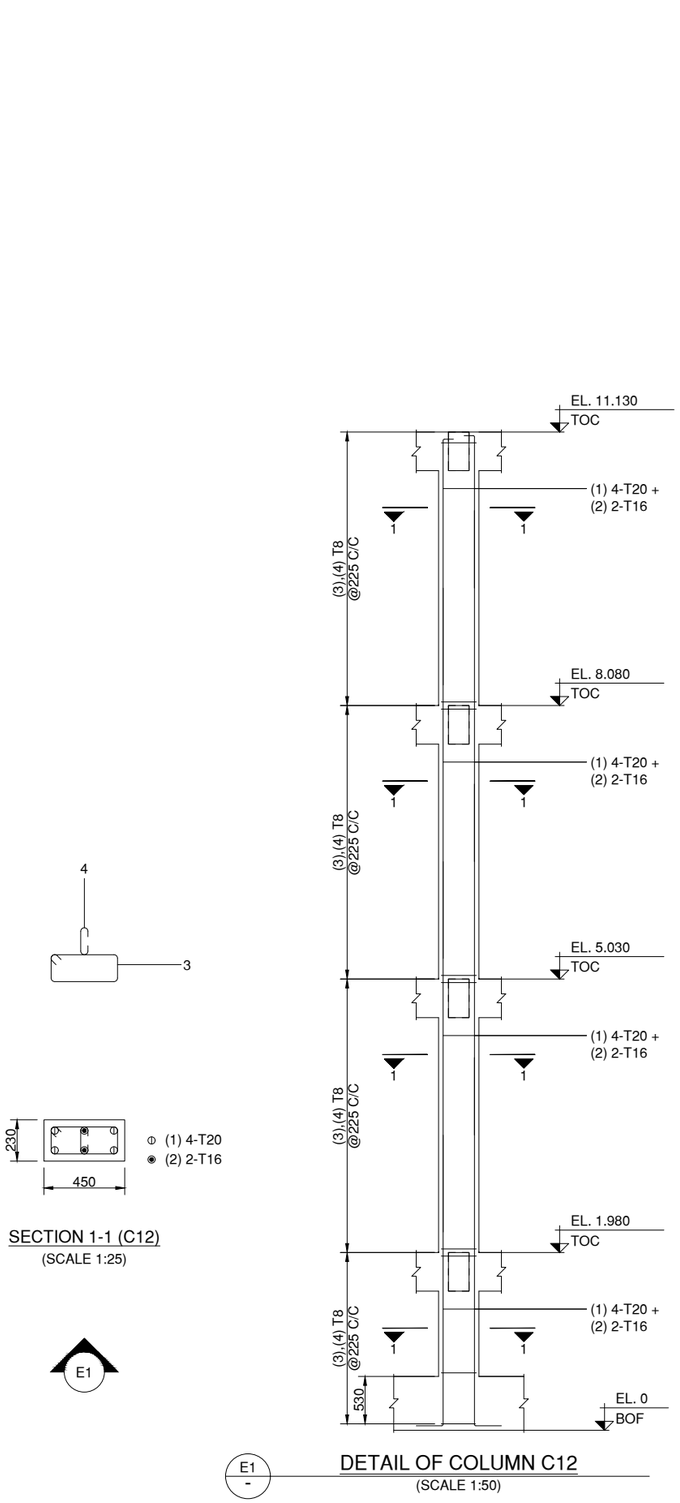

SECTION 1-1 (C12)
(SCALE 1:25)

E1
-
DETAIL OF COLUMN C12
(SCALE 1:50)

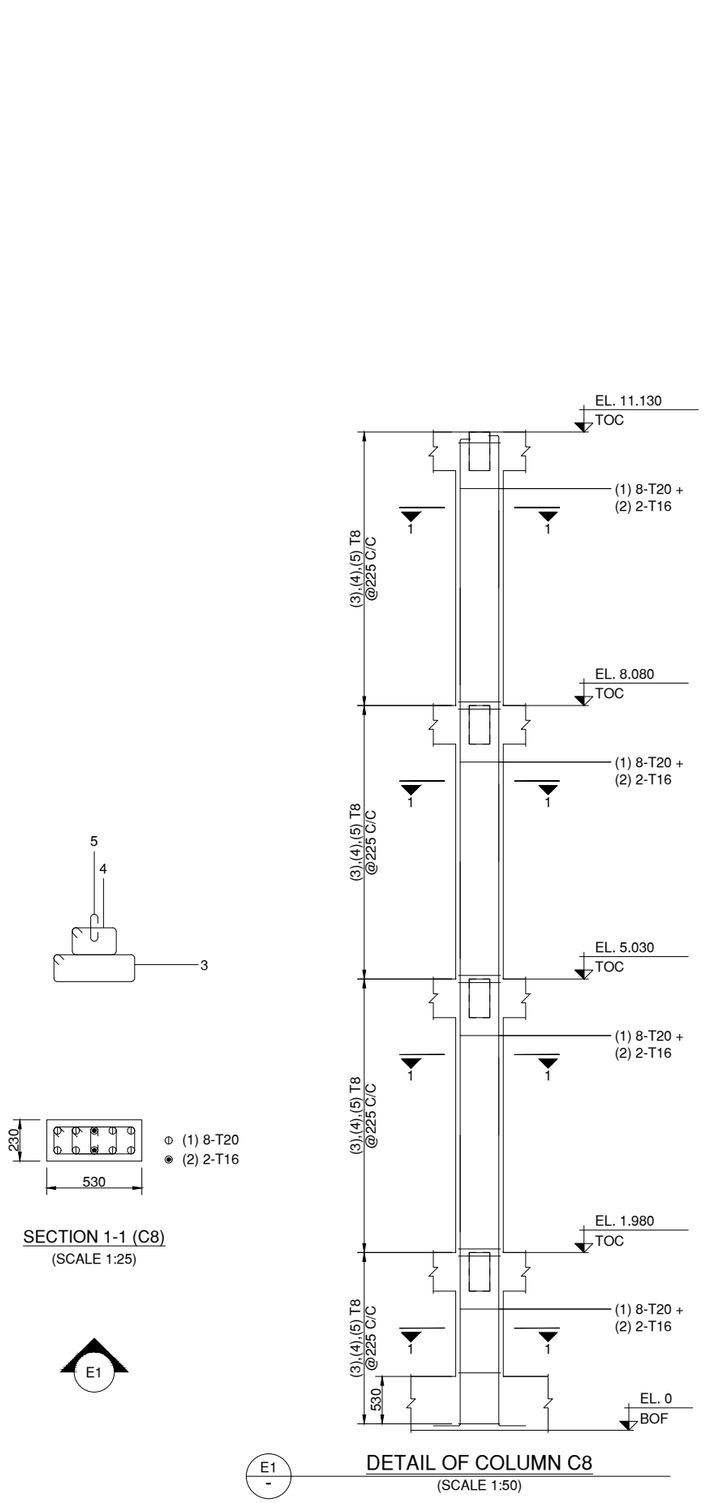

SECTION 1-1 (C8)
(SCALE 1:25)

E1
-
DETAIL OF COLUMN C8
(SCALE 1:50)

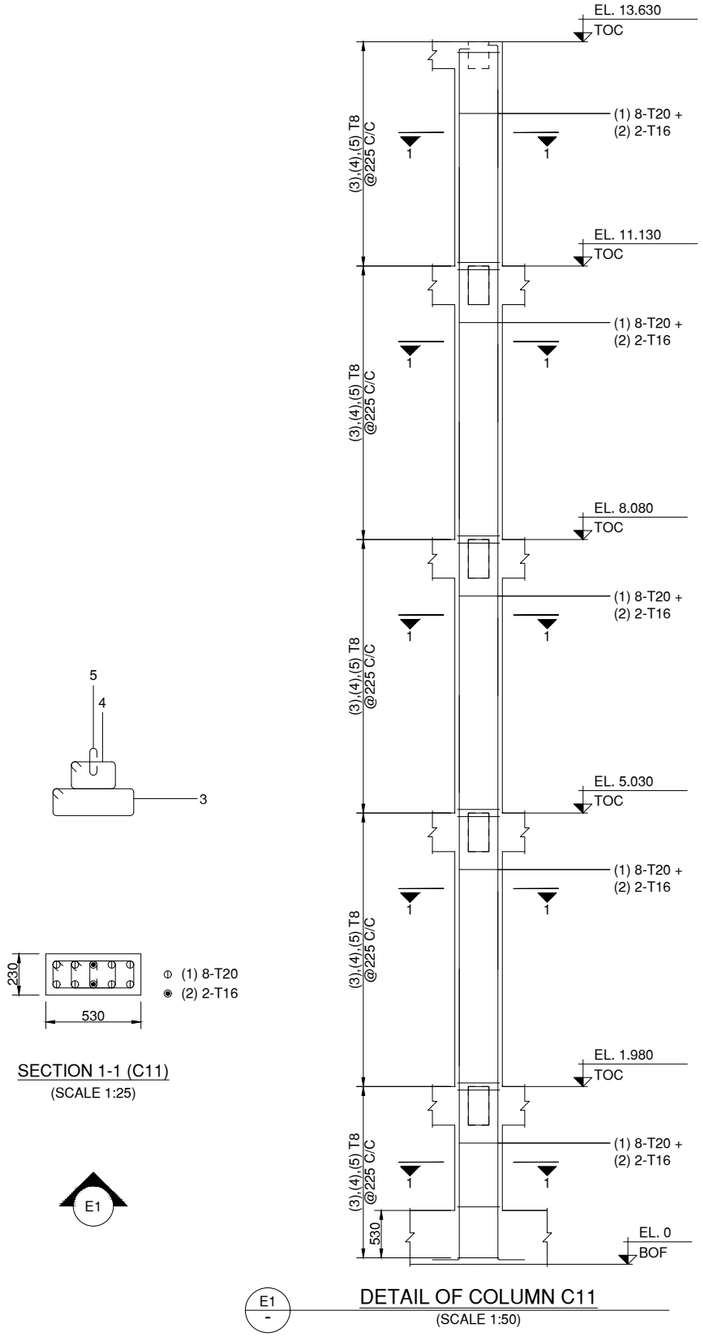

SECTION 1-1 (C11)
(SCALE 1:25)

E1
-
DETAIL OF COLUMN C11
(SCALE 1:50)