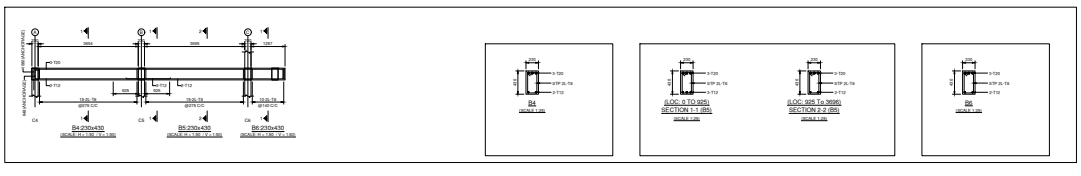
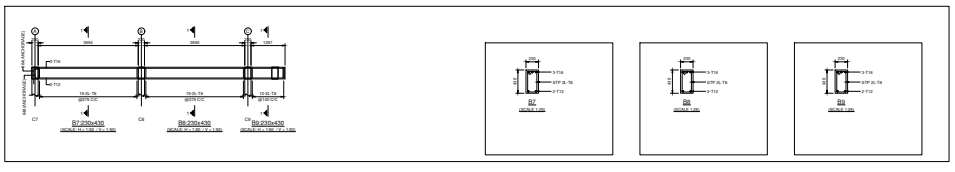
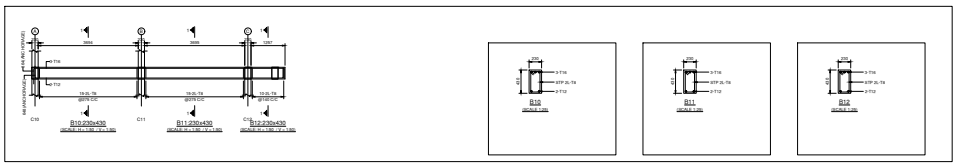
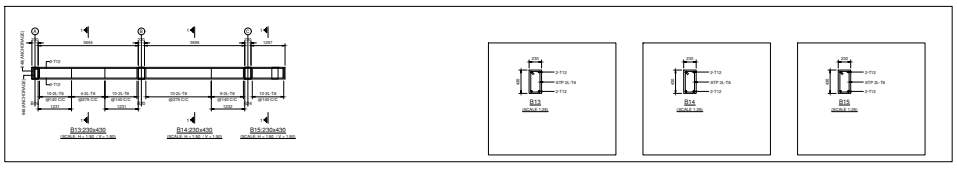
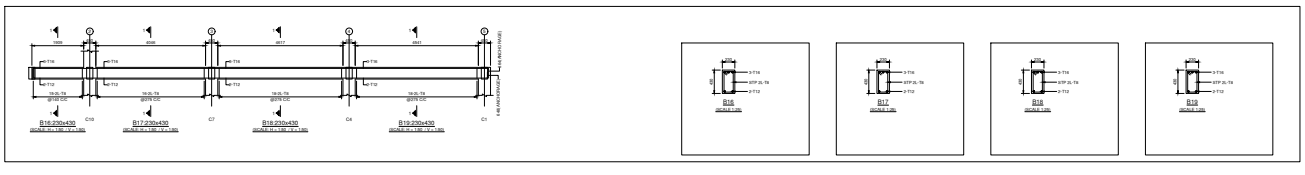

B1:230x430
B2:230x430
B3:230x430
B1
B2
B3

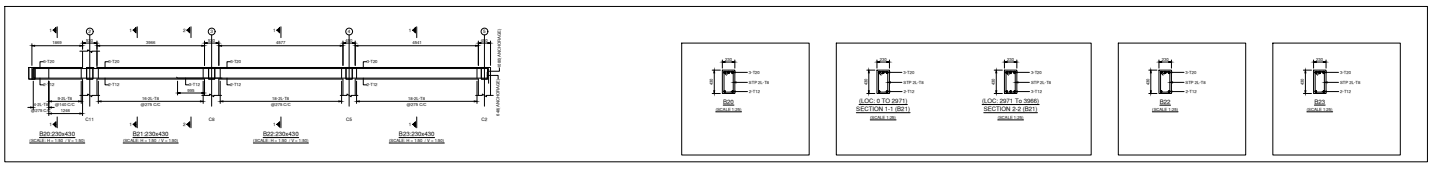

B4:230x430
B5:230x430
B6:230x430
B4
(LOC: 0 TO 925)
SECTION 1-1 (B5)
(LOC: 925 To 3696)
SECTION 2-2 (B5)
B6

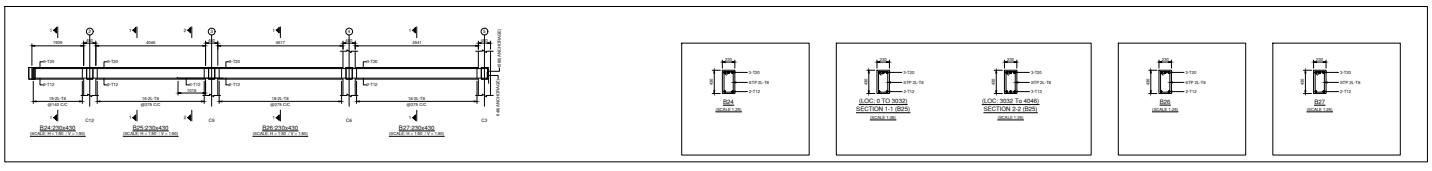

B7:230x430
B8:230x430
B9:230x430
B7
B8
B9

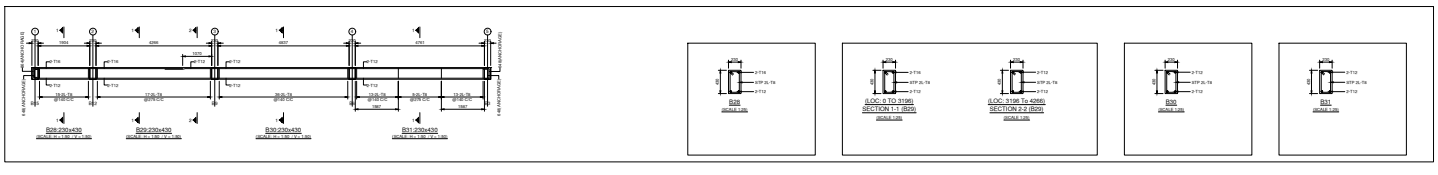

B10:230x430
B11:230x430
B12:230x430
B10
B11
B12


B13:230x430
B14:230x430
B15:230x430
B13
B14
B15


B16:230x430
B17:230x430
B18:230x430
B19:230x430
B16
B17
B18
B19


B20:230x430
B21:230x430
B22:230x430
B23:230x430
B20
(LOC: 0 TO 2971)
SECTION 1-1 (B21)
(LOC: 2971 To 3996)
SECTION 2-2 (B21)
B22
B23


B24:230x430
B25:230x430
B26:230x430
B27:230x430
B24
(LOC: 0 TO 3032)
SECTION 1-1 (B25)
(LOC: 3032 To 4046)
SECTION 2-2 (B25)
B26
B27


B28:230x430
B29:230x430
B30:230x430
B31:230x430
B28
(LOC: 0 TO 3196)
SECTION 1-1 (B29)
(LOC: 3196 To 4266)
SECTION 2-2 (B29)
B30
B31