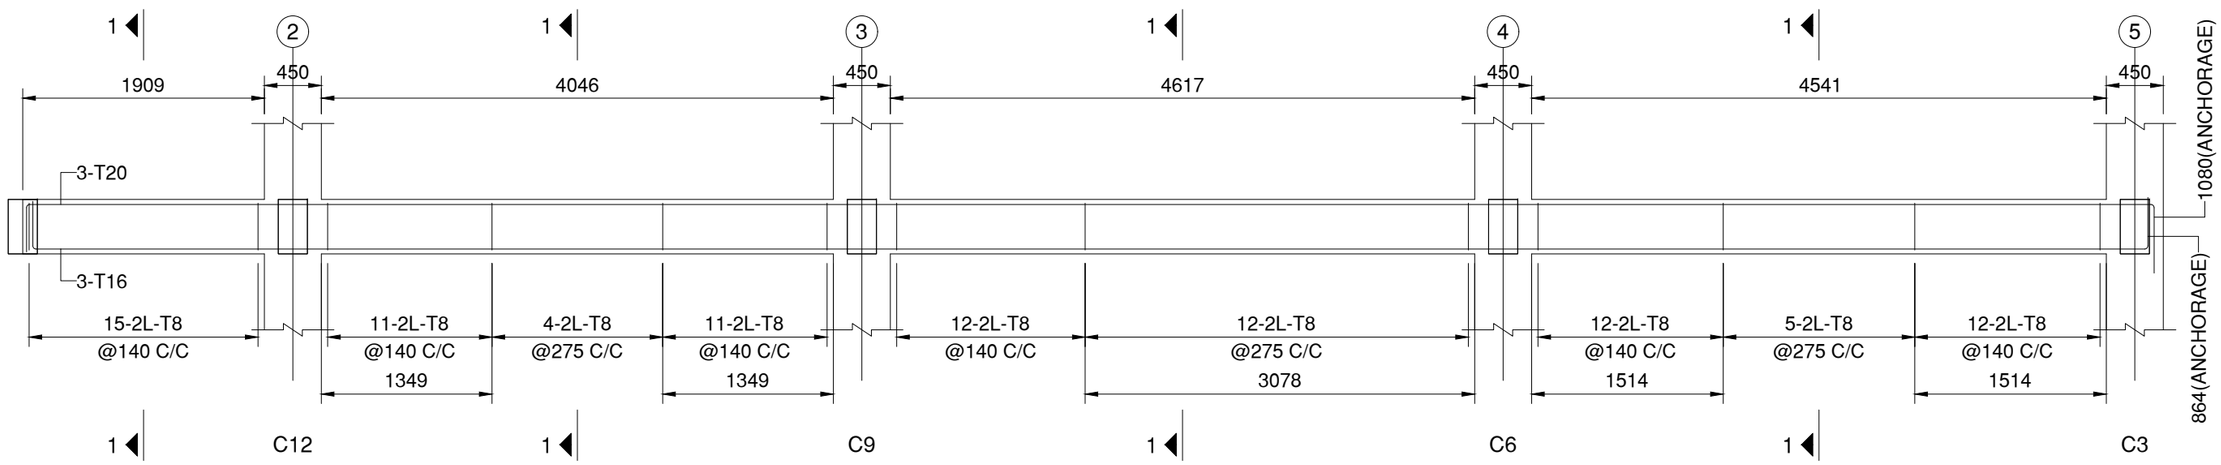

B24:230x430
(SCALE: H = 1:50 / V = 1:50)

B25:230x430
(SCALE: H = 1:50 / V = 1:50)

B26:230x430
(SCALE: H = 1:50 / V = 1:50)

B27:230x430
(SCALE: H = 1:50 / V = 1:50)