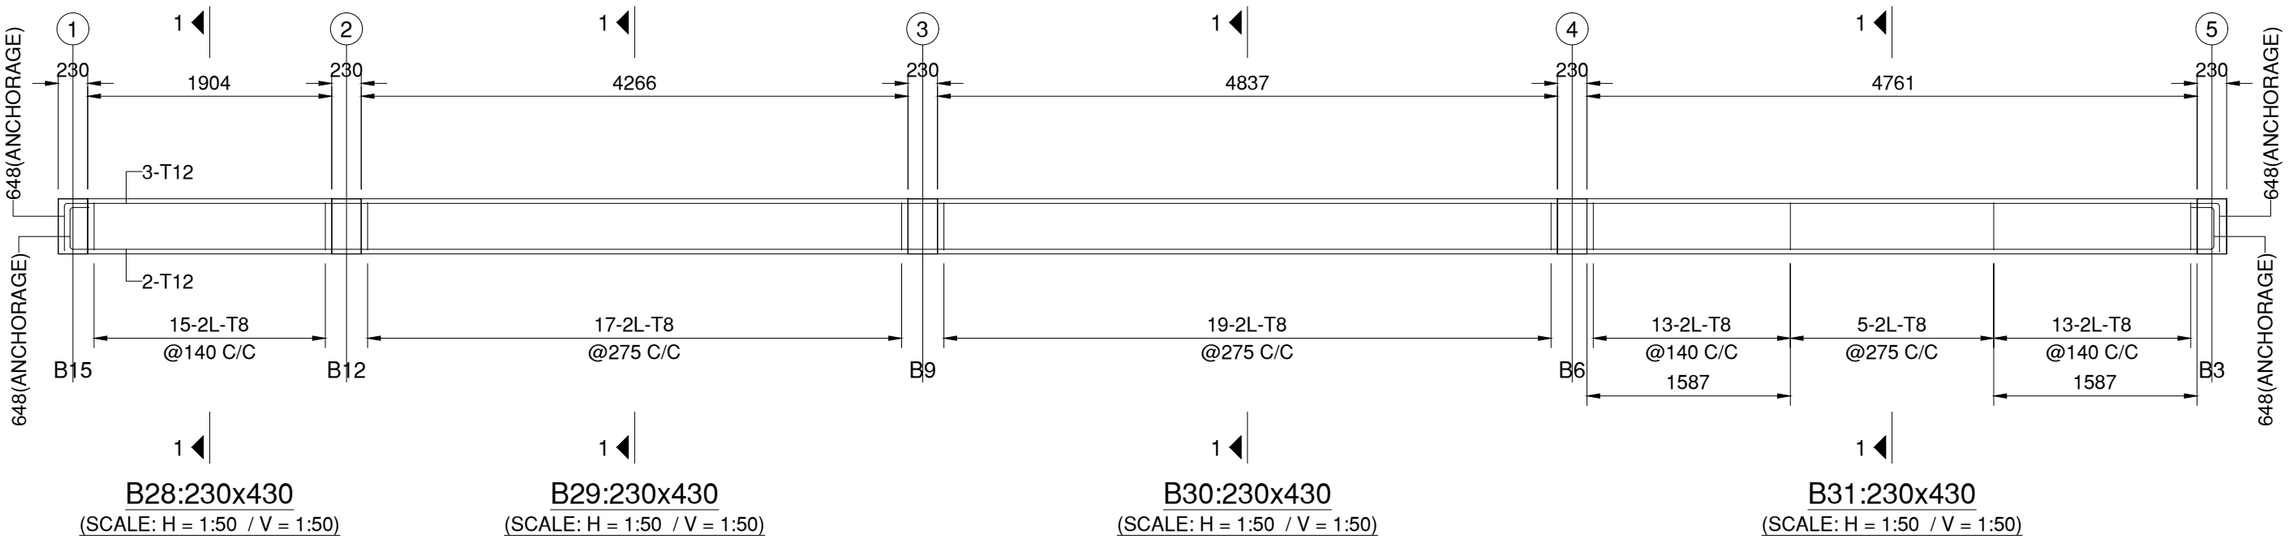

B28:230x430
(SCALE: H = 1:50 / V = 1:50)

B29:230x430
(SCALE: H = 1:50 / V = 1:50)

B30:230x430
(SCALE: H = 1:50 / V = 1:50)

B31:230x430
(SCALE: H = 1:50 / V = 1:50)