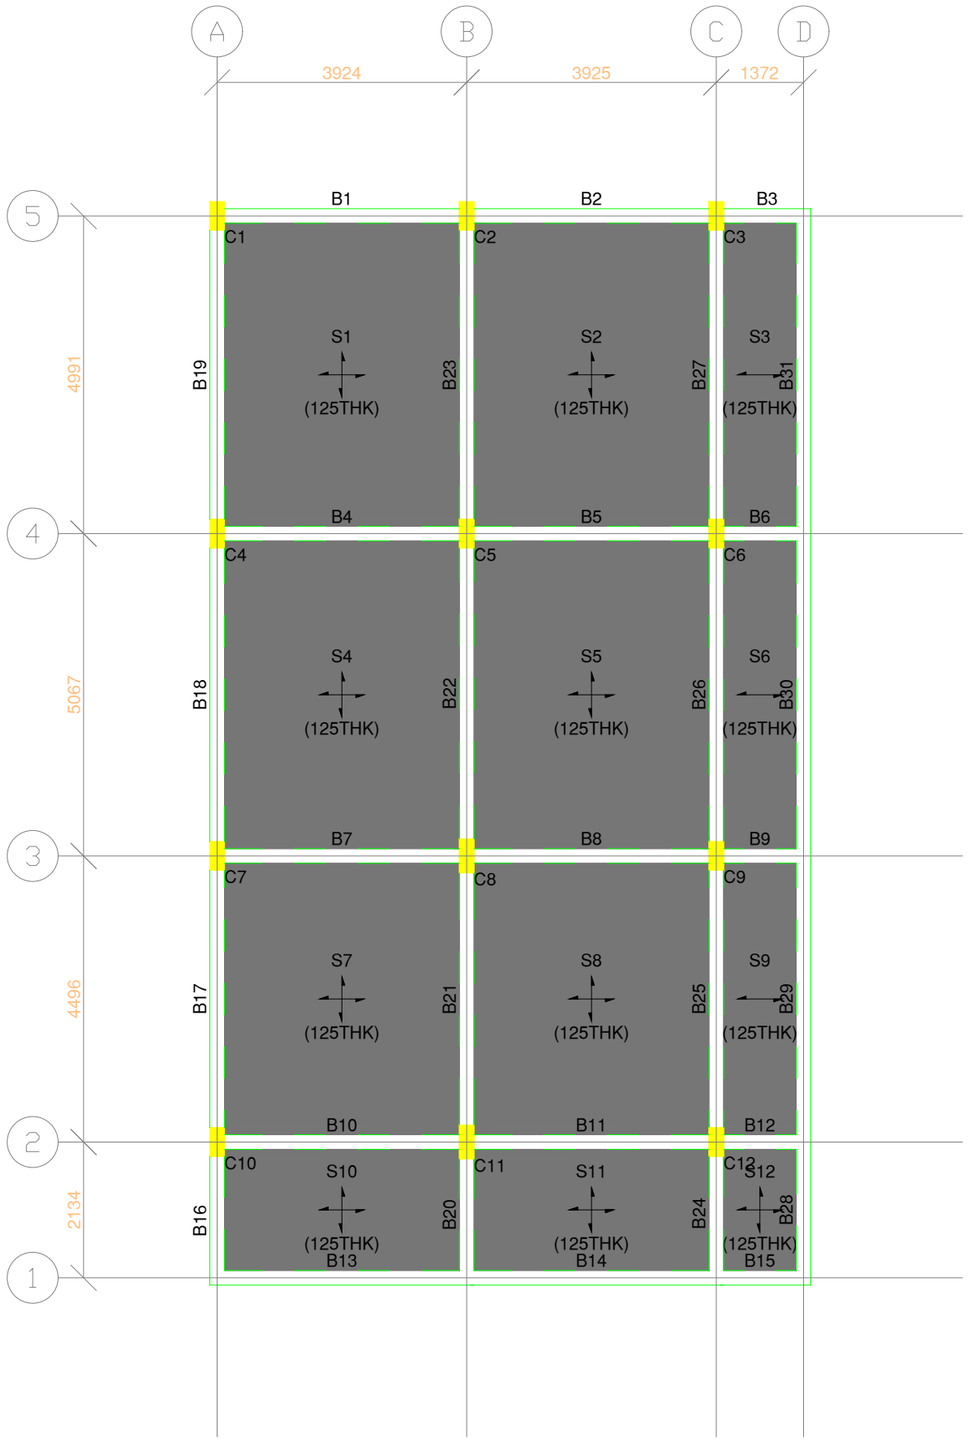

PLAN AT 5.029 M

BEAM LEGEND

BEAM	SIZE	
	B	D
B1,B2,B3,B4,B5,B6,B7,B8,B9,B10,B11 B12,B13,B14,B15,B16,B17,B18,B19 B20,B21,B22,B23,B24,B25,B26,B27 B28,B29,B30,B31	230	430