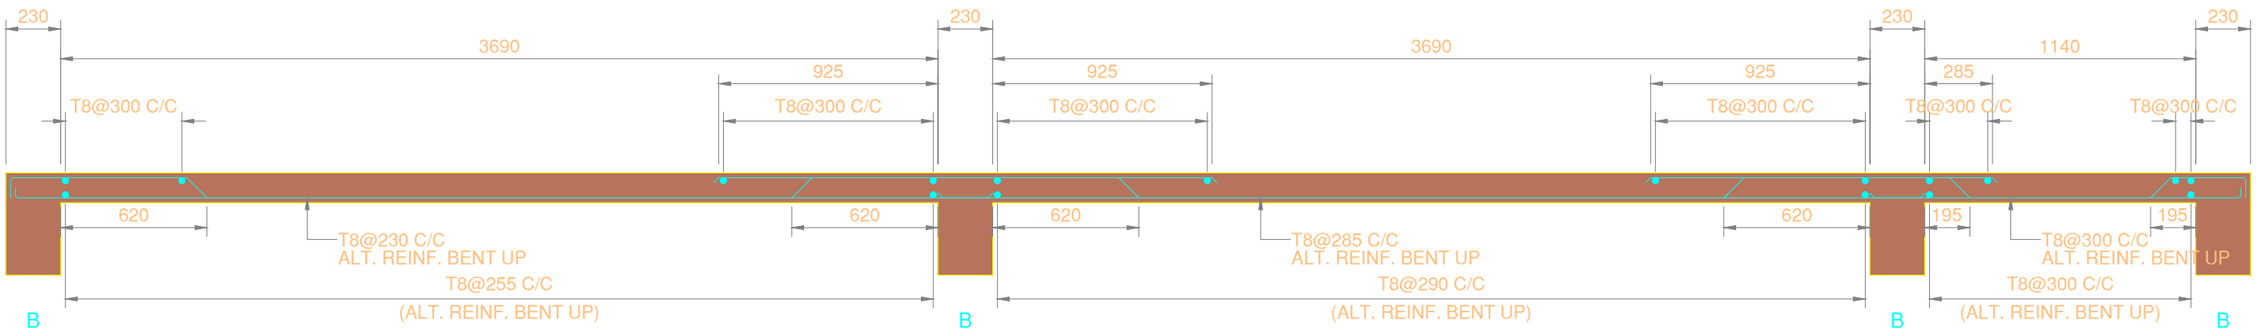

SLAB S1

(TWO WAY) (125 THK)

SLAB S2

(TWO WAY) (125 THK)

SLAB S3

(ONE WAY) (125 THK)

SECTION 1-1