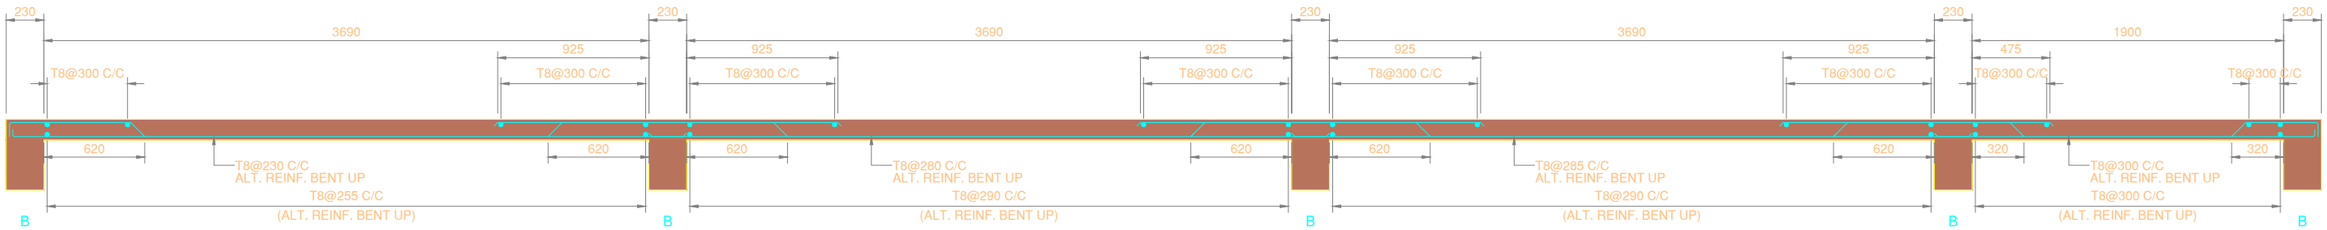
230
3690
925
T8@300 C/C
620
T8@230 C/C
ALT. REINF. BENT UP
T8@255 C/C
(ALT. REINF. BENT UP)
B
SLAB S1
(TWO WAY) (125 THK)
T8@280 C/C
ALT. REINF. BENT UP
T8@290 C/C
SLAB S4
T8@285 C/C
SLAB S7
475
1900
320
T8@300 C/C
SLAB S10

SECTION A-A