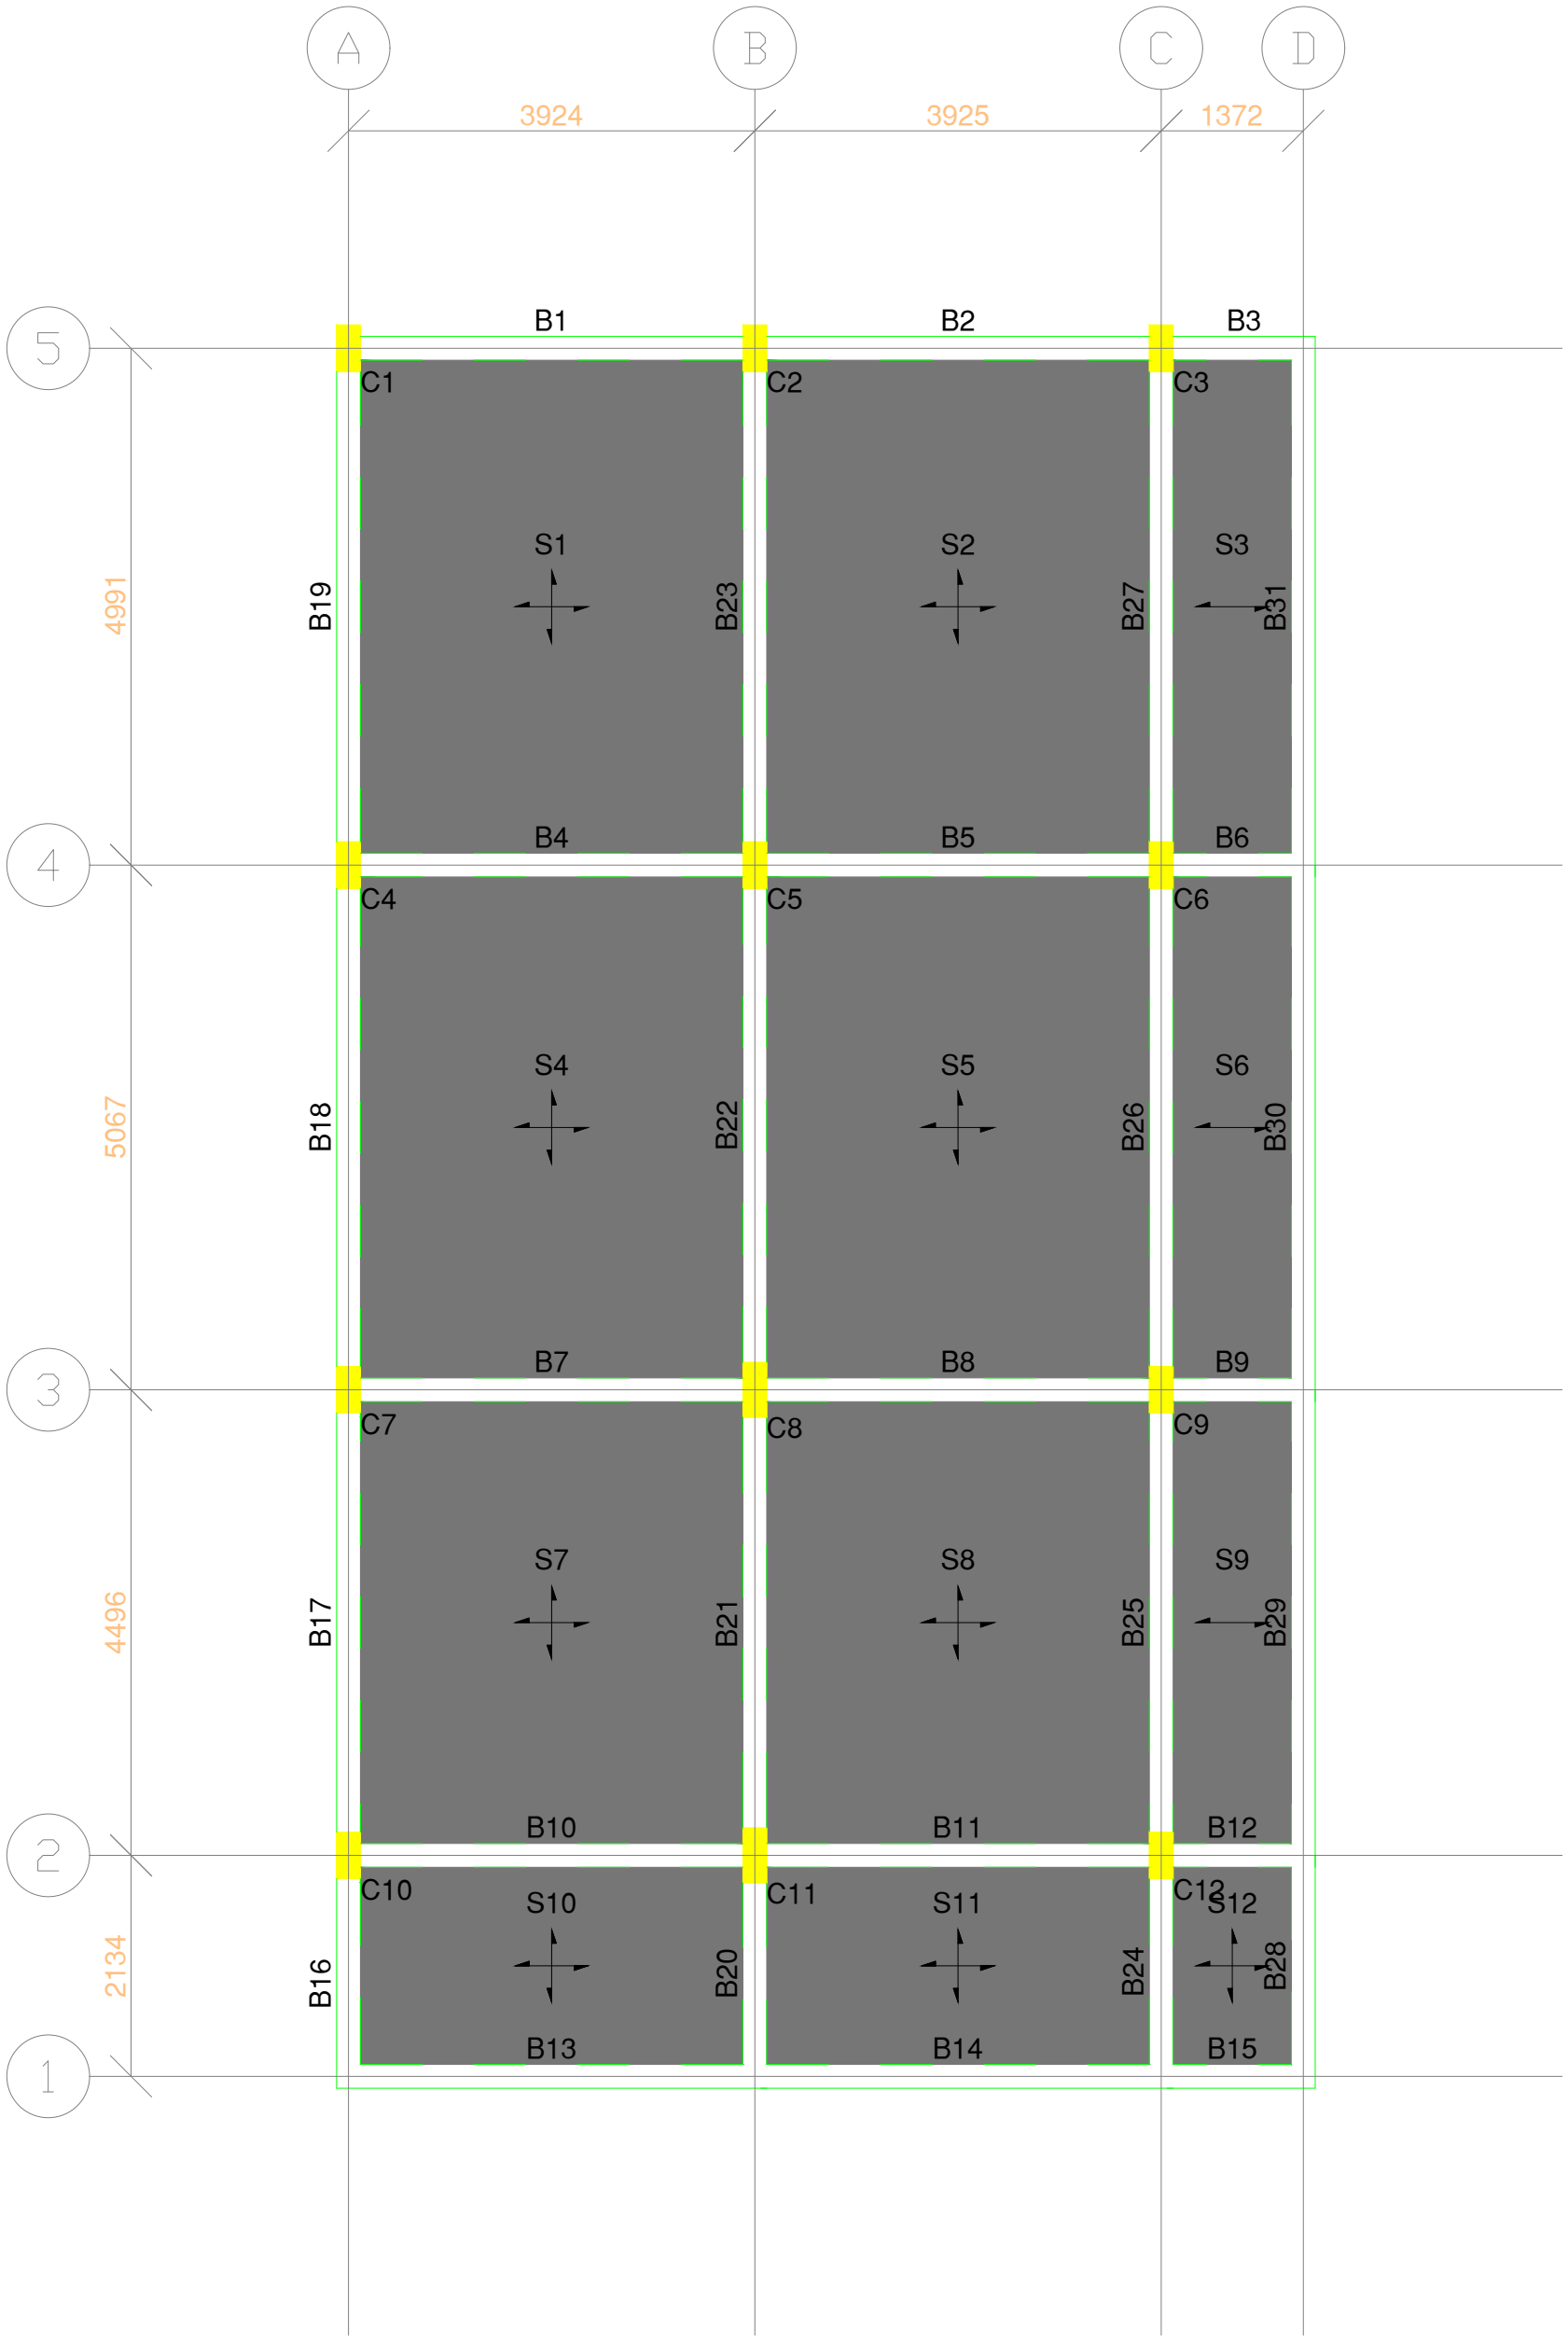

PLAN AT 8.077 M