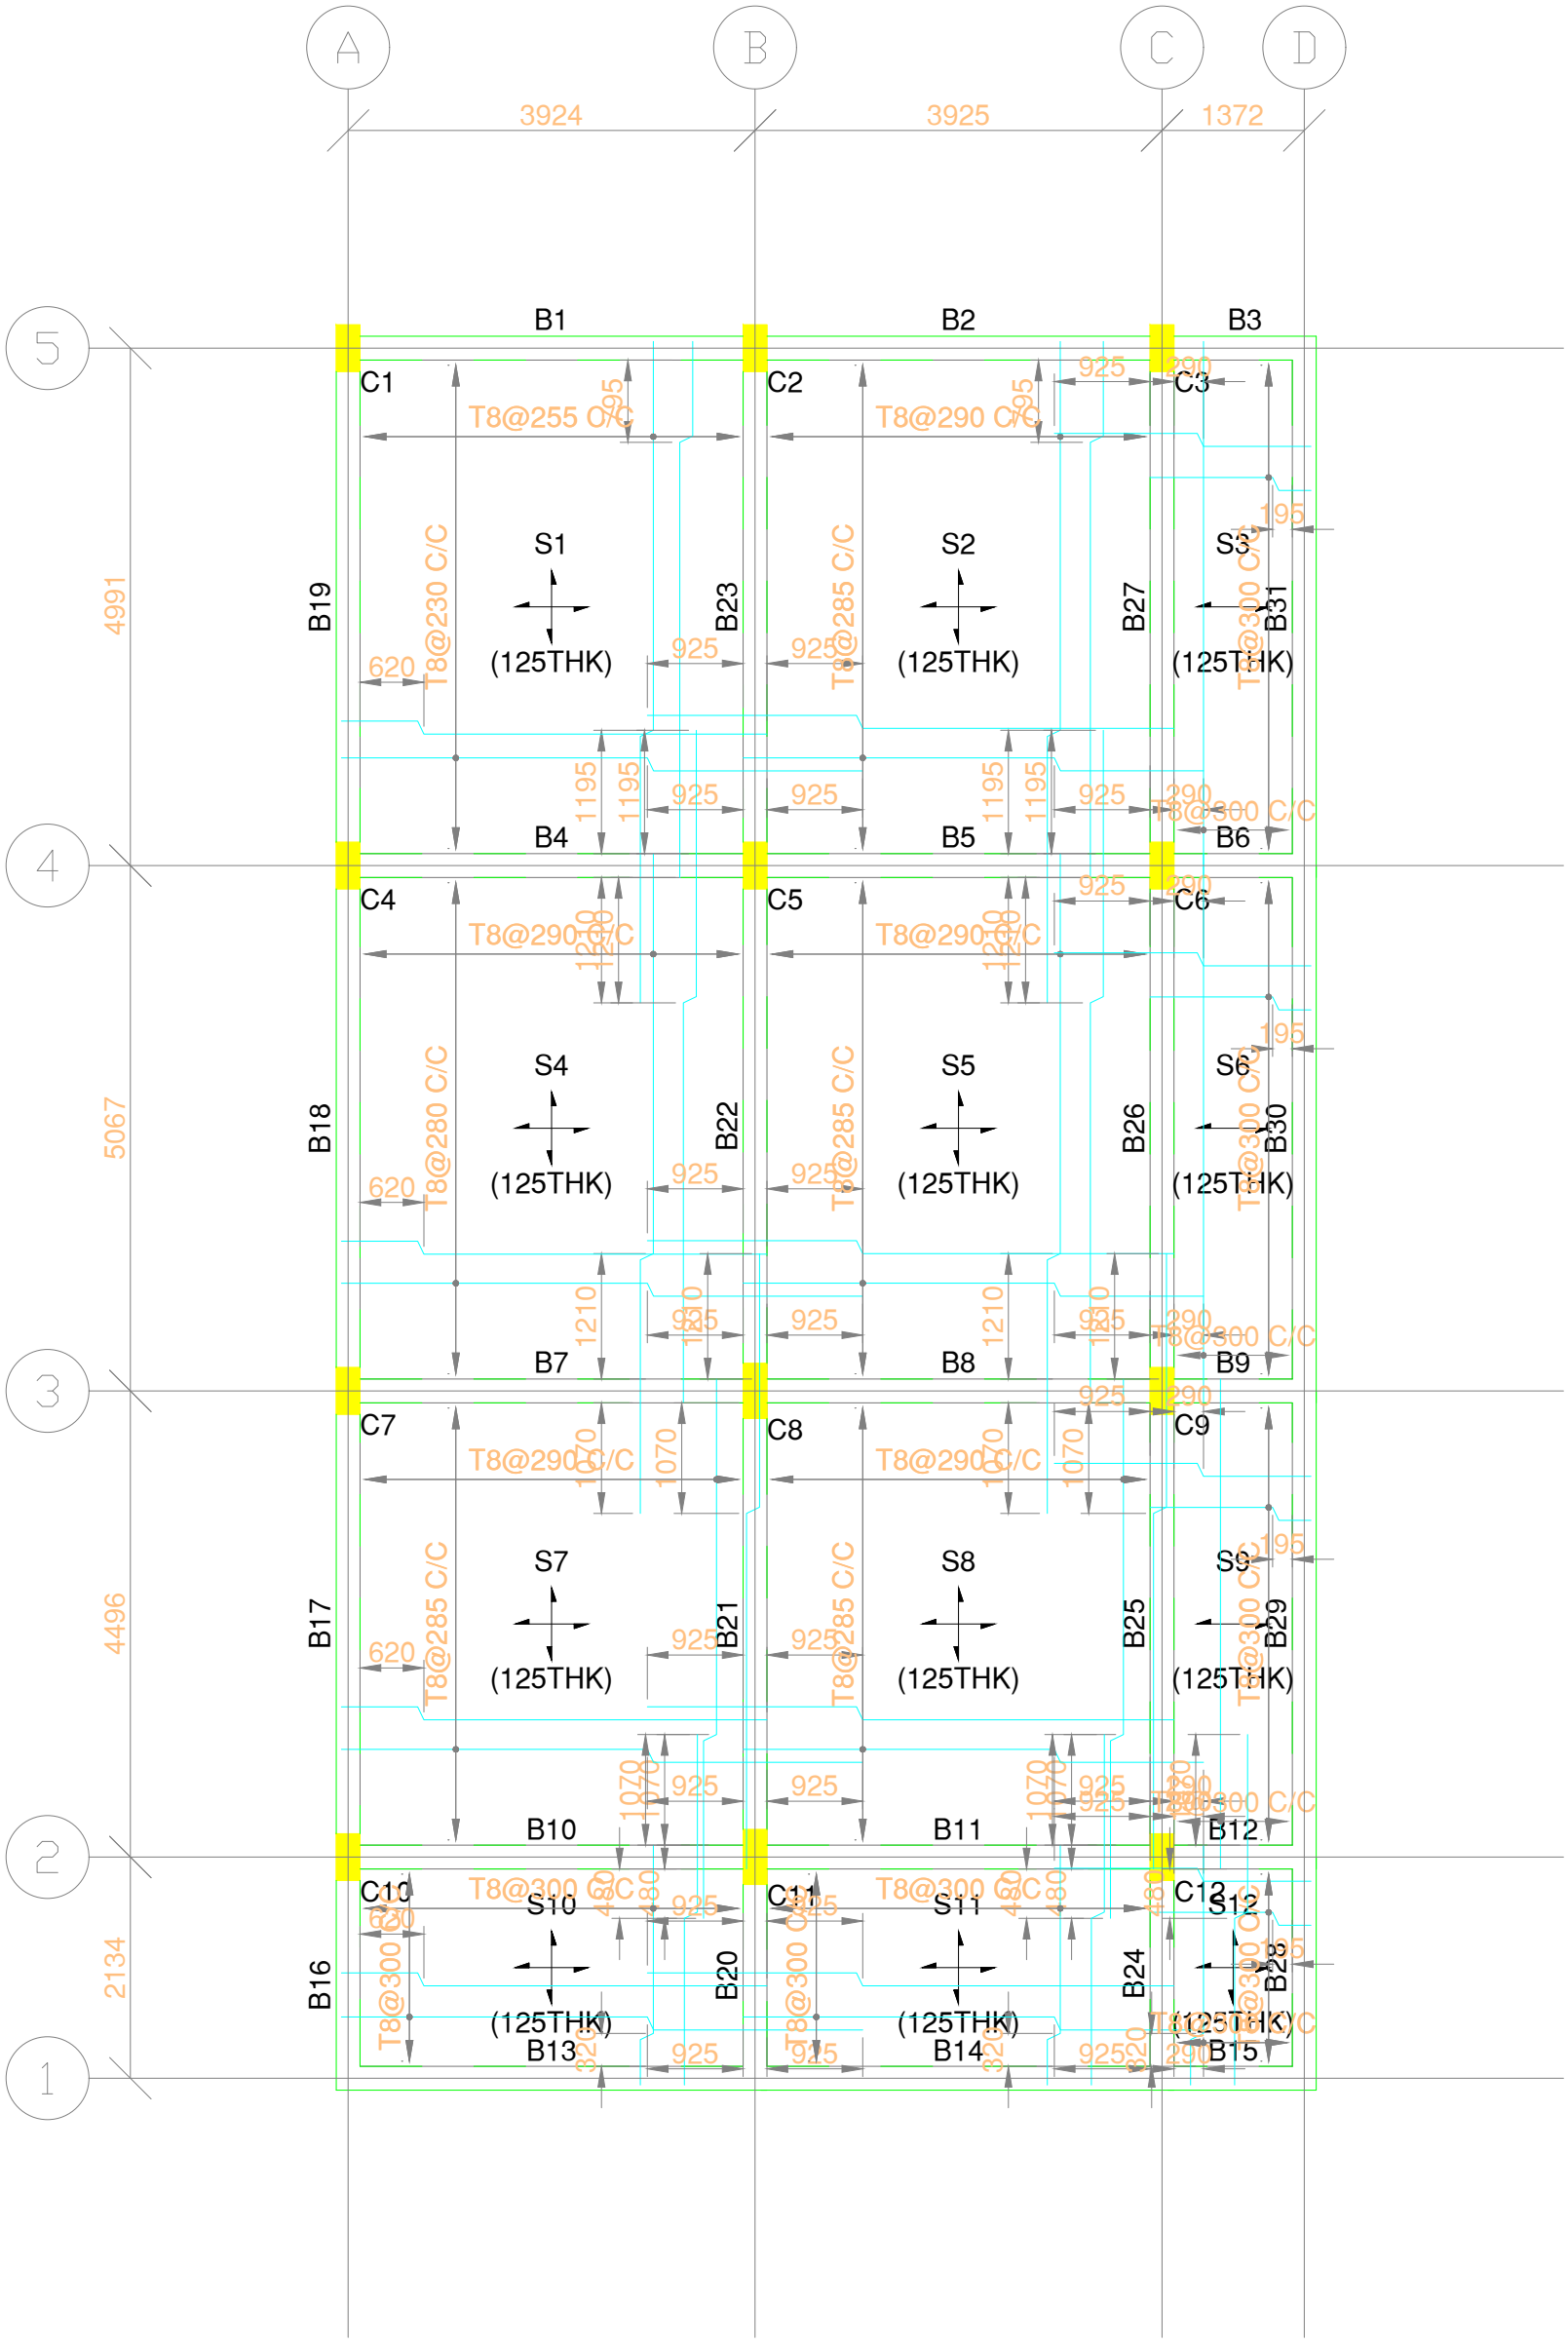

BENTUP REINFORCEMENT LAYOUT - 11.125 M

(SCALE: H = 1:100 / V = 1:100)