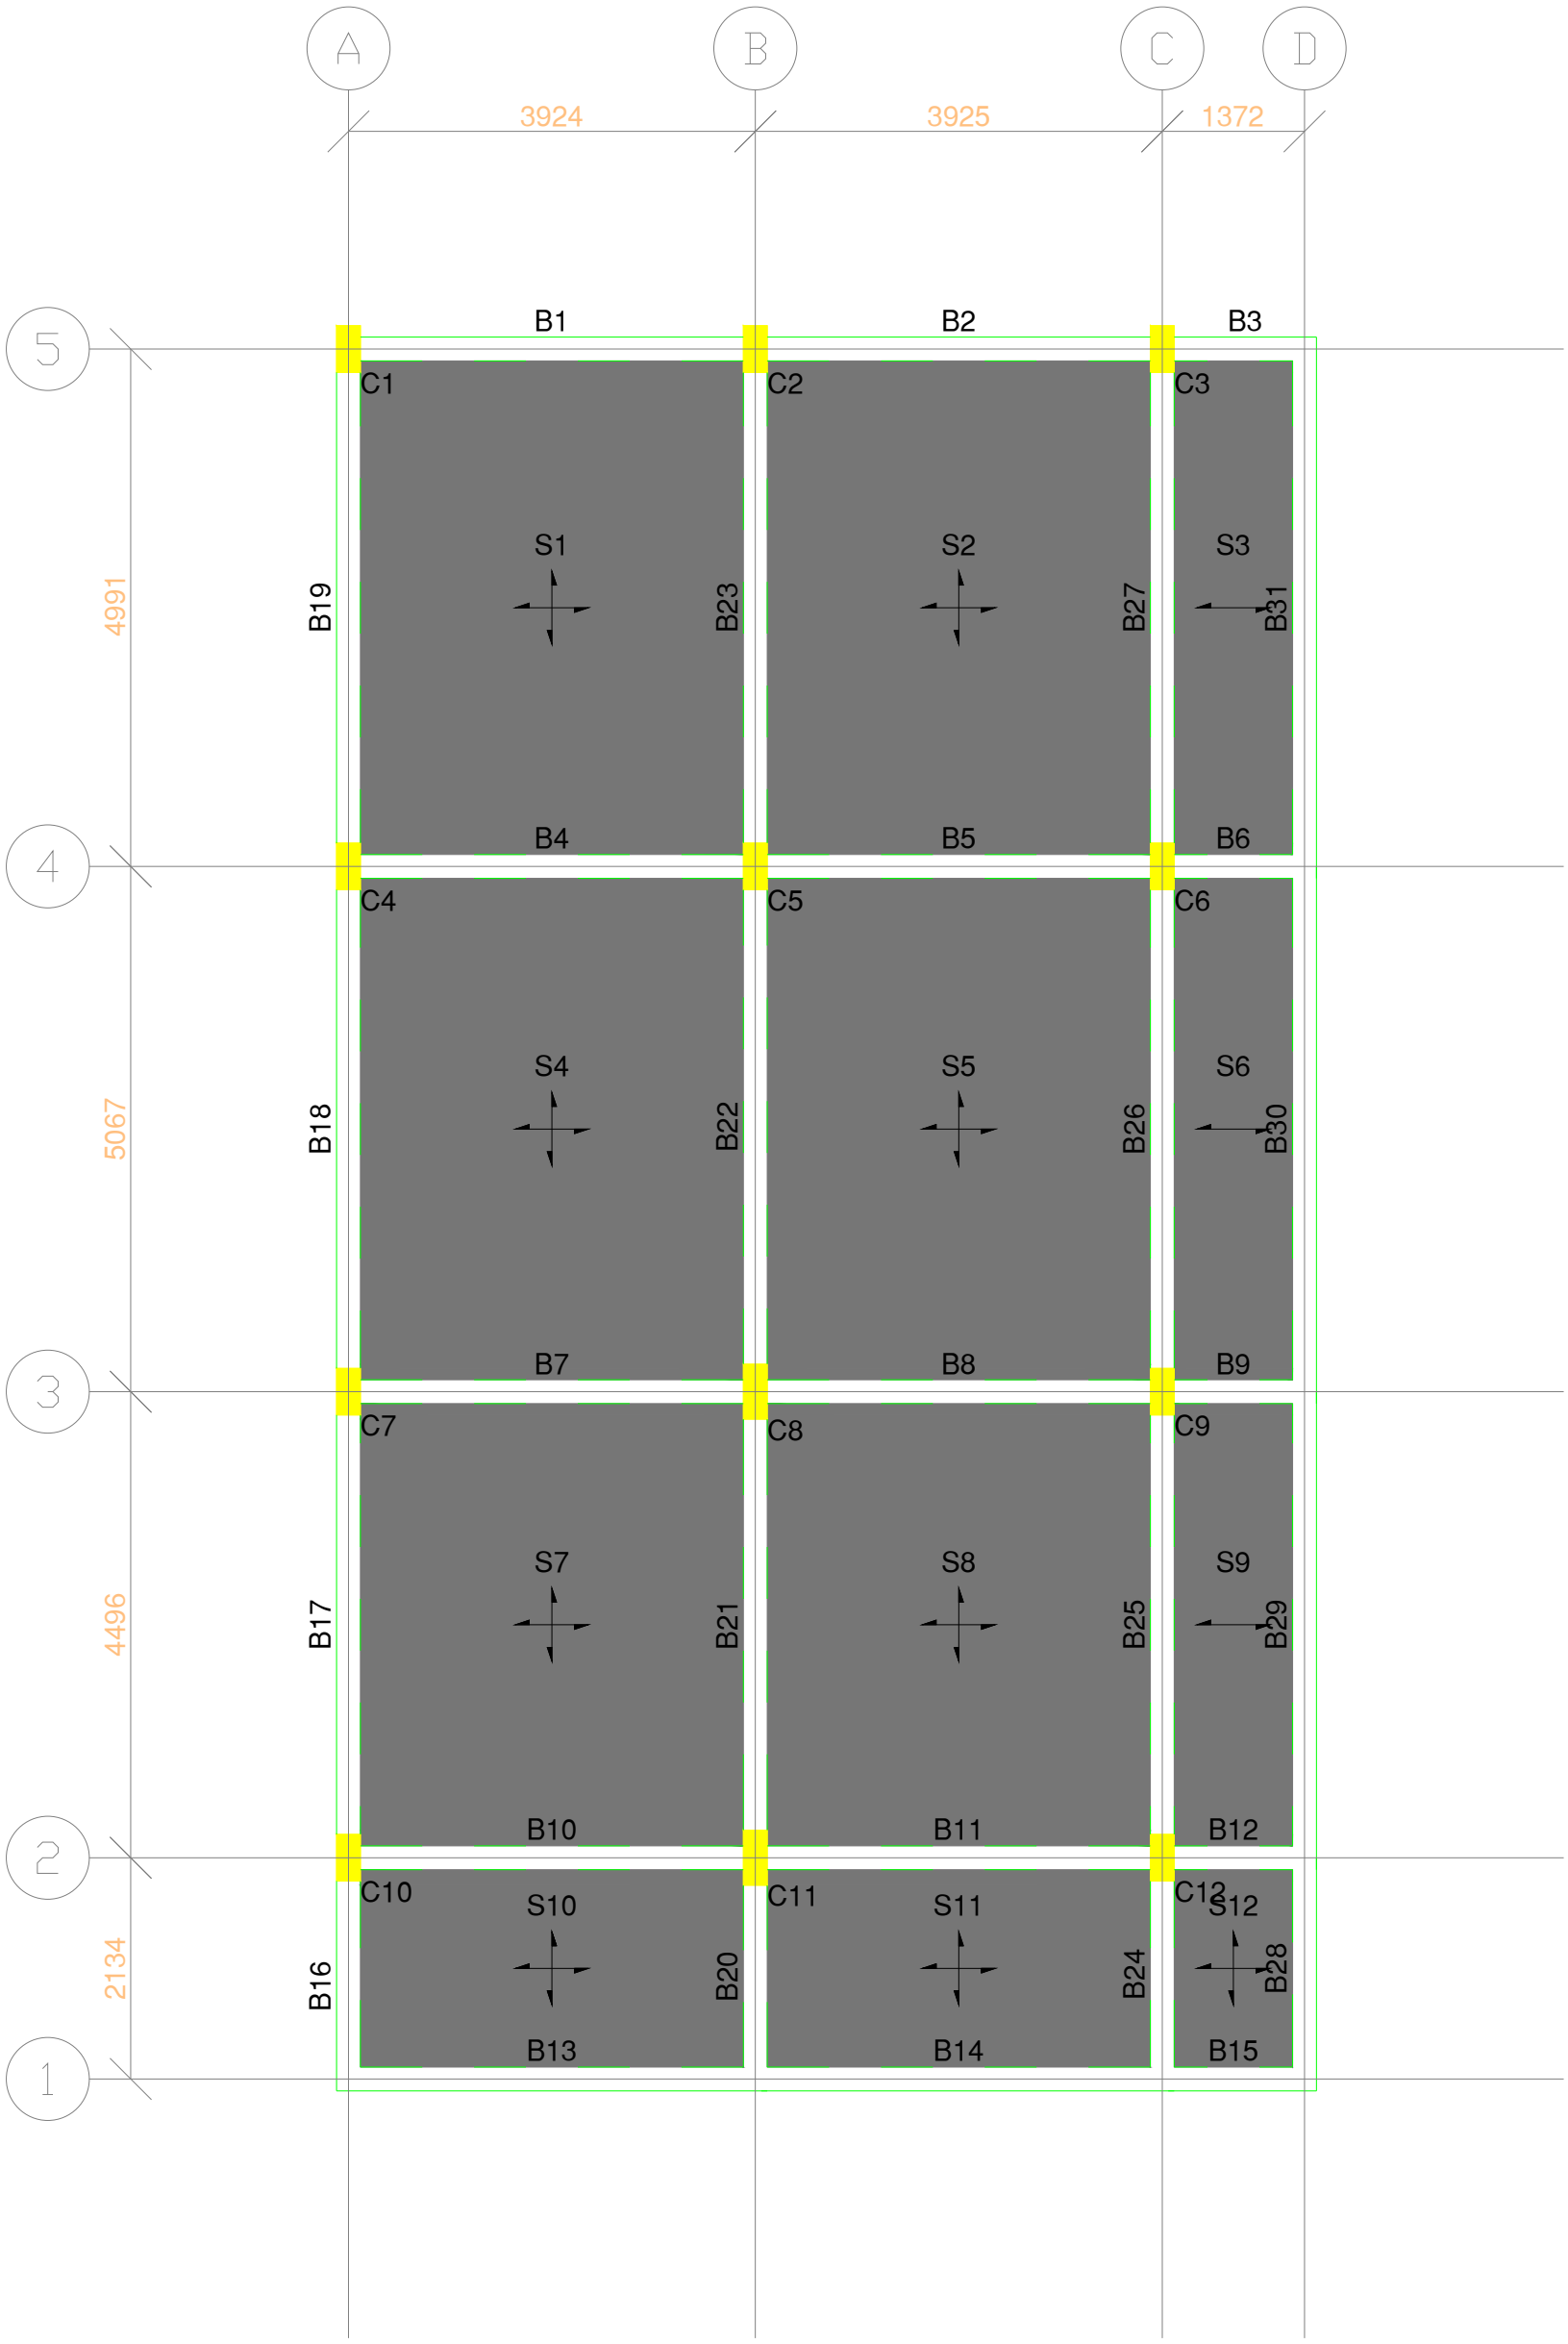

PLAN AT 11.125 M