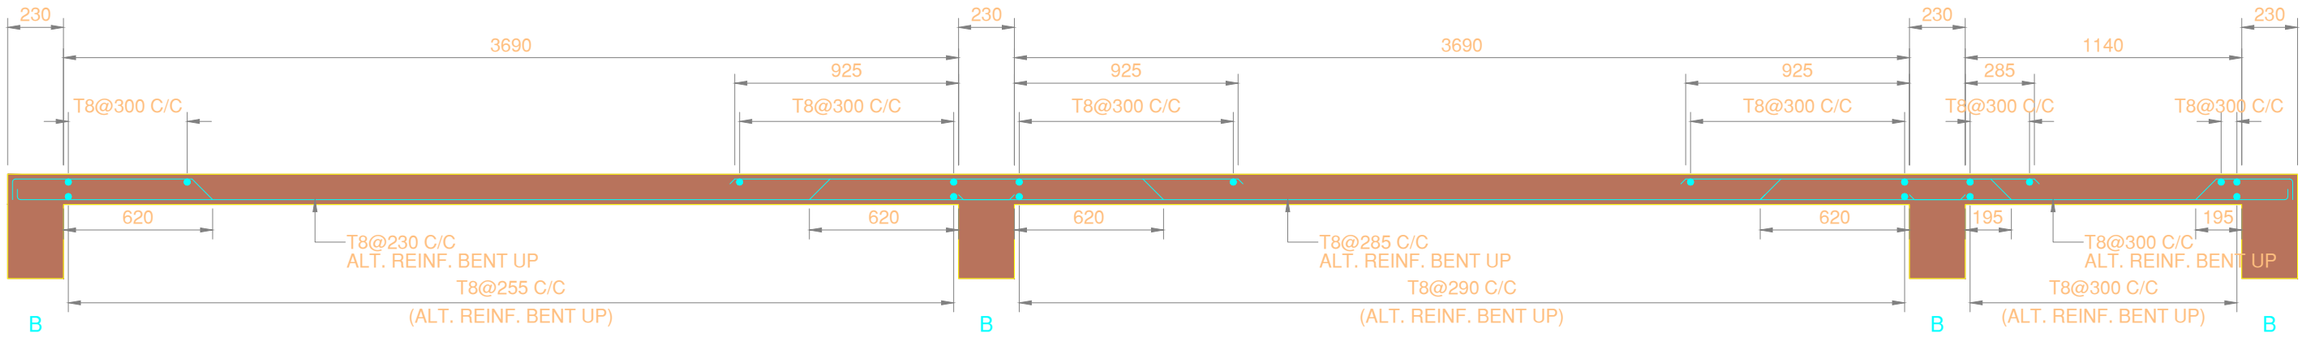
230
3690
925
T8@300 C/C
620
T8@230 C/C
ALT. REINF. BENT UP
T8@255 C/C
B
SLAB S1
(TWO WAY) (125 THK)
230
925
T8@300 C/C
620
T8@285 C/C
ALT. REINF. BENT UP
T8@290 C/C
B
SLAB S2
(TWO WAY) (125 THK)
230
3690
925
T8@300 C/C
620
195
T8@300 C/C
ALT. REINF. BENT UP
T8@300 C/C
B
SLAB S3
(ONE WAY) (125 THK)
230
1140
285
T8@300 C/C
195
T8@300 C/C
ALT. REINF. BENT UP
B

## SECTION 1-1